
YEAR 1 ARCHITECTURE PORTFOLIO

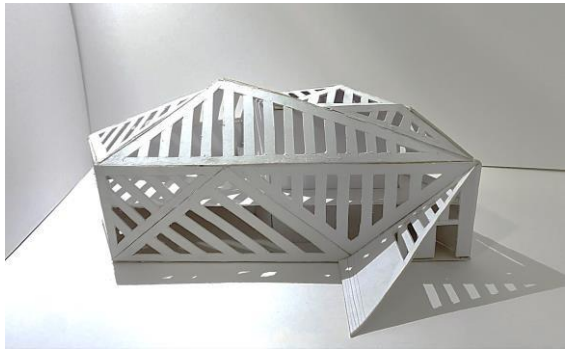


# DERIN ENHOS


# MODULE:
# DESIGN STUDIO PROJECT I






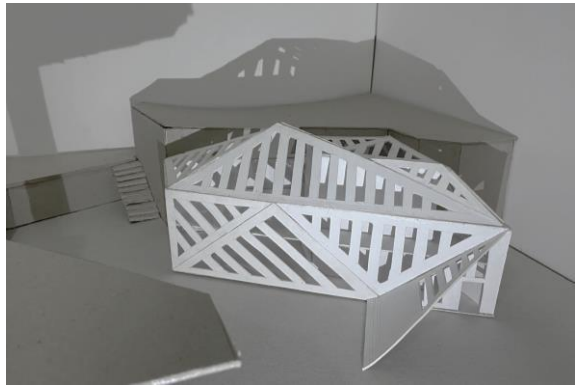



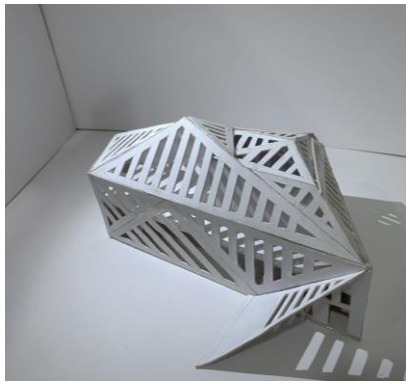

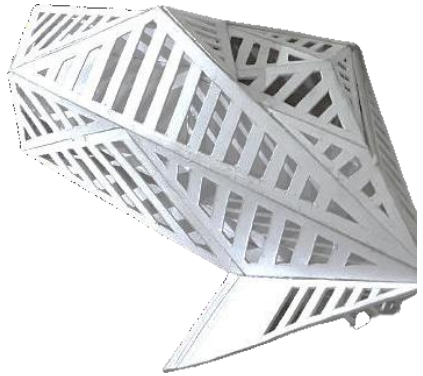

# Design Studio – Project 1

## *Nottingham Youth Hub*

Project 1: Designing a building to be used as a youth hub in Nottingham.

# Site Sections + Elevations – Hand Drawn

SITE ANALYSIS - elevation drawings 1:200

Elevation D-D




SITE ANALYSIS - section drawings 1:200

Section A-A



SITE ANALYSIS - section drawings 1:200

Section B-B

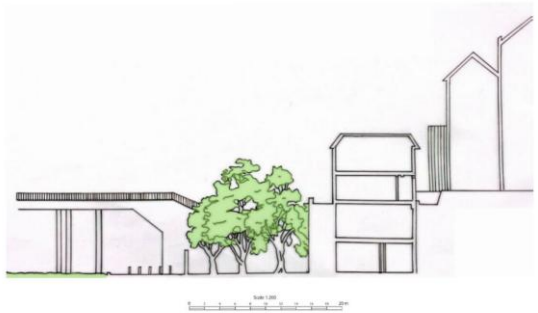

SITE ANALYSIS - elevation drawings 1:200


Elevation C-C



# Site Analysis – Hand Drawn

## SITE ANALYSIS- materiality analysis

Looking at the materials surrounding the site gives a better understanding of the type of architectural style the neighbouring buildings have, and why certain decisions were taken to use certain materials, styles, or colours. With a better understanding of the feel of the atmosphere and surroundings there is more clarity on what types of structures and forms will fit in or stand out, which types of materials would clash or match the surroundings. Designing with respect and consideration to surrounding structures is neccesary for a suitable design that would attract the correct target market.

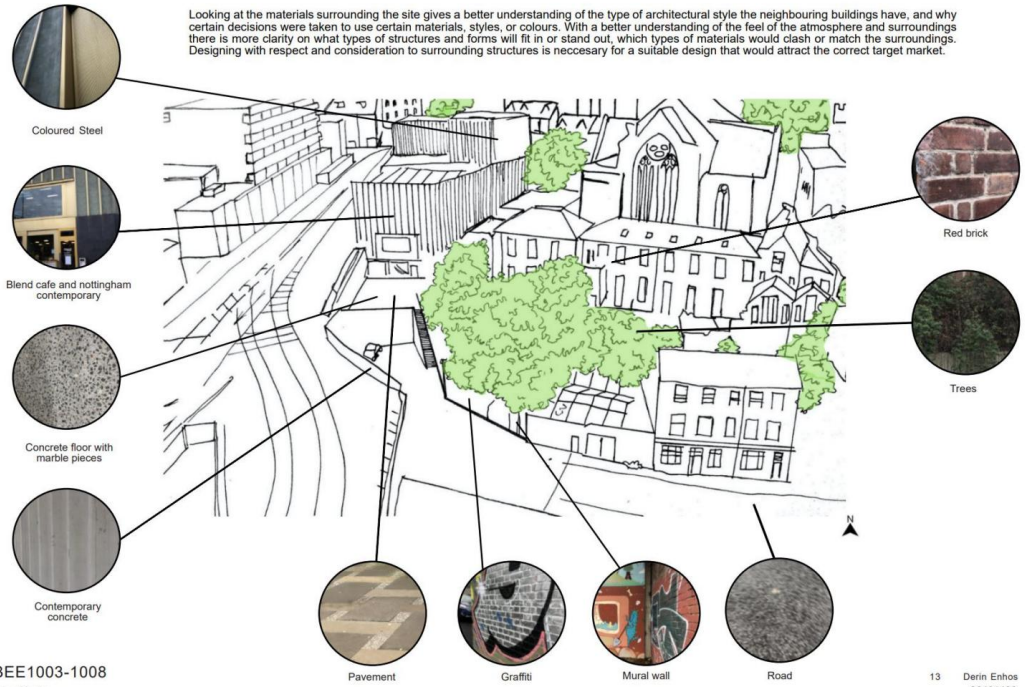



ABEE1003-1008
Design Studio



## SITE ANALYSIS- accessibility and key views

This site (site D) was chosen for the brief as it is located next to many public servies and areas in which people commute and use on a daily basis. The site lies below the Nottingham Tramway, near the Nottingham Railway station and just before the Lace Market tram stop. This allows for many clients to easily access the site and visit the services surrounding the site on a daily basis. Being surrounded by different options of transport ensures the site will be visited and used sufficiently.

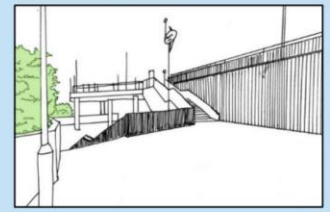

Northern stairs approach

From the north of the site, people will approach from the stairs going down from Nottingham Contemporary at level with Blend cafe, making a scenic walk leading up to the site with a cafe to dine in.



Eastern street approach

From the east, there is a road until the posts where people can access the site by car, pedestrian or cycle. It is a less busy enterance to the site with the view of the skatepark staight ahead and Fletchers Theatre on the left. Calmer and quieter approach to the site.



Northern street approach

From the back of the site, in front of Nottingham Contemporary and the Chapel (Pitcher and Piano) people can access the site by car, cycling or walking. The walk in between the two buildings and down the stairs is set in a very urban setting, it is busier and there is more to see.



Shown at a larger scale (1:1250) are the methods of transport in the area that the site is located in. The blue highlight marks the Nottingham Tramway for transport by tram and the green highlight marks normal roads for transport by car.

The site is accessible from 4 different areas;

1. The stairs above the skatepark from the Tramway- above site, pedestrian (facing south)

2. The staircase from Nottingham contemporary - above site, pedestrian (facing northwest)

3. The road in front of Fletchers Theatre - vehicular, cycle access (facing east)

4. The pathway downwards from the skate park towards Nottingham College - pedestrian (facing southeast)



View facing north

The majority of the site is covered with trees and the southern elevation of the site borders the unitarian chapel as seen on the photo. The photo was taken facing north.




View facing south

This photo was taken on top of the first set of stairs facing the set of stairs that lead to the Nottingham tramway. Walking northwest leads to the Lace Market Tram stop.

ABEE1003-1008
Design Studio


# Client Analysis


## CLIENT ANALYSIS- client narrative

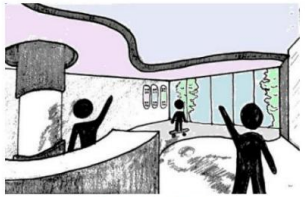
Reception/enterance


Cafe/food court


Netted lounge/library area

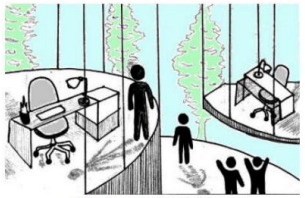
Office/manager/supervisor area

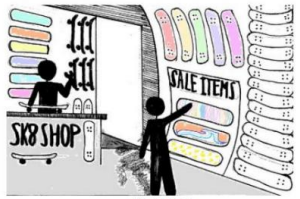

Skate shop



Arcade/games room



Screening video edits



Seminar/competition room



Rooftop gym/parkour section


## ERGONOMICS- ergonomic studies

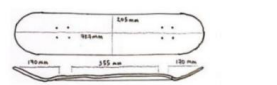

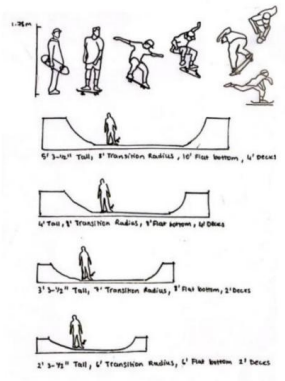

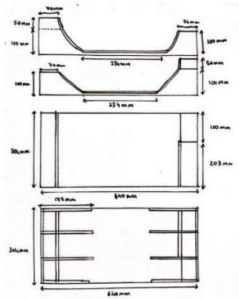

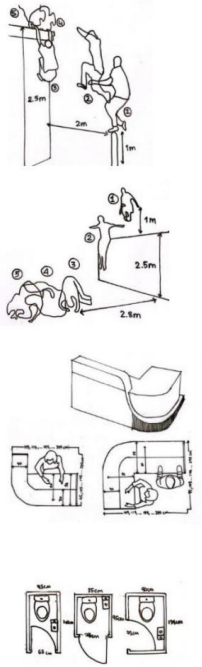

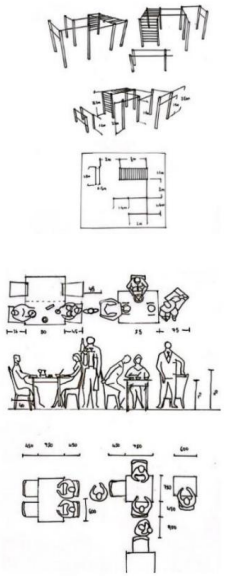

# Inspiration and Concept Model + Sketches

INSPIRATION- Lebbeus Woods drawings










- Lebbeus Woods was an influential architect and artist known for his visionary architectural drawings.
- His drawings often depicted futuristic and unconventional architectural concepts and speculative designs.
- Woods' drawings were characterized by their intricate and detailed linework, combining both precise technical elements and expressive, gestural strokes.
- He used a variety of mediums, including ink, graphite, and watercolor, to create his drawings, each contributing to the unique visual impact of his work.
- Woods' drawings explored themes of transformation, resilience, and the relationship between architecture and the socio-political context.
- His designs often challenged conventional notions of space, structure, and function, pushing the boundaries of what architecture could be.
- Woods' drawings were not merely representations of built structures but also expressed broader philosophical and conceptual ideas.
- He often incorporated elements of chaos, disruption, and asymmetry in his drawings, reflecting his belief that architecture should respond to the dynamic and unpredictable nature of the world.
- Woods' drawings have been widely exhibited and published, and they continue to inspire architects, artists, and designers around the world.
- His unique approach to architectural representation has had a profound impact on the field, emphasizing the importance of imagination, experimentation, and the power of drawings as tools for exploring new possibilities in architecture.

Referring back to my touchstone, the two drawings I made were inspired by Lebbeus Woods' art style.

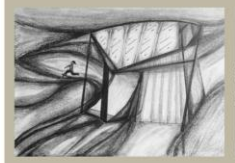




TOUCHSTONE - brainstorming ideas/concept

Punk culture - youth movement - informality - different not conforming to stereotypical ideas of a building. Rebeling societal norms.

- Subculture that emerged in the mid-1970s, primarily in the United Kingdom and the United States.
- Characterized by its DIY (Do It Yourself) ethos, anti-establishment attitude, and rejection of mainstream norms.
- Influenced by various art forms, including music, fashion, visual arts, and literature.
- Focused on individualism, self-expression, and authenticity.
- Often associated with loud, fast-paced music genres like punk rock.
- Embraced a raw and unpolished aesthetic in both music and style.
- Challenged societal norms, consumerism, and conformity.
- An expression of discontent with the status quo and traditional norms.
- Punk rebellion often targeted authority figures, governments, and institutions.
- Rejecting the idea of blindly following rules and systems.
- Utilized music as a powerful tool for protest and social commentary.
- Engaged in provocative and controversial behavior to shock and challenge society.

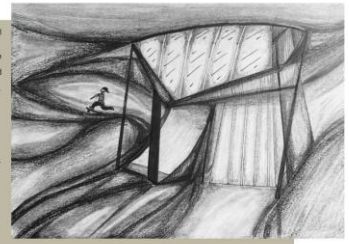




In terms of design, this concept would take form as being a building that is so architecturally different from its surrounding buildings on site. A structure that will stand out, look like its out of place and doesn't belond there.


Like a loud and bold statement piece. Confident piece of architecture that shows off the anti-establishment and rebellion attitude that comes along with being young.


A youth hub that encourages adventure and being unique.

PROCESS- concept models and sketches

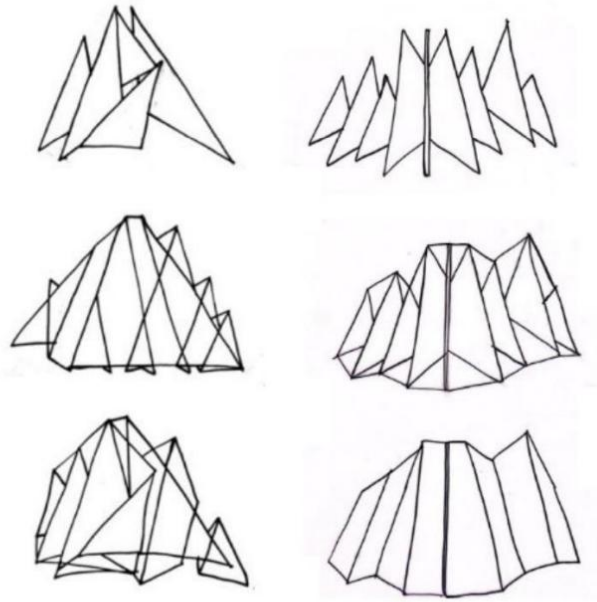


I initially took inspiration from the complex forms showcased in the 'Morphosis Models' and used the inspiration to start coming up with ideas for the form of the building. I decided to vaguely start sketching different abstract facade ideas that present the idea of informality and not following usual building facades that are presented throughout the site as I wanted to create architecture that stands out from its surroundings, almost looking out of place. I made a concept model showcasing my initial response to the inspiration from my precedents and touchstone.

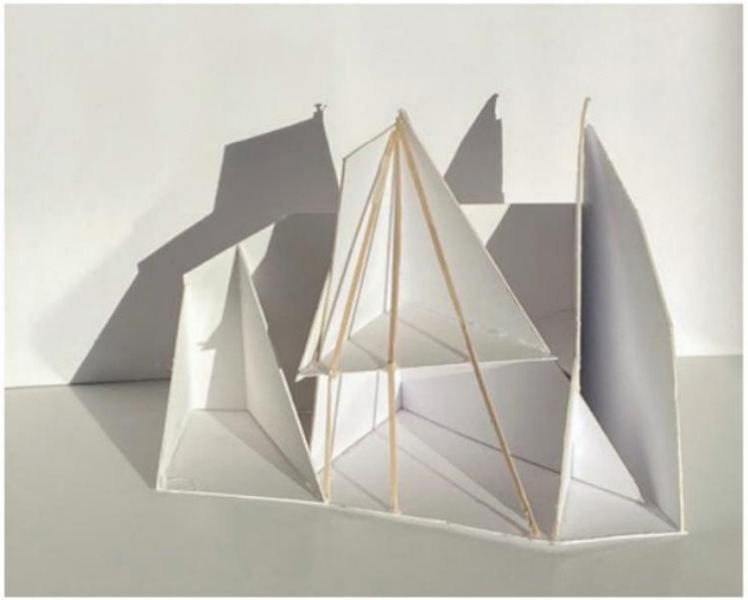

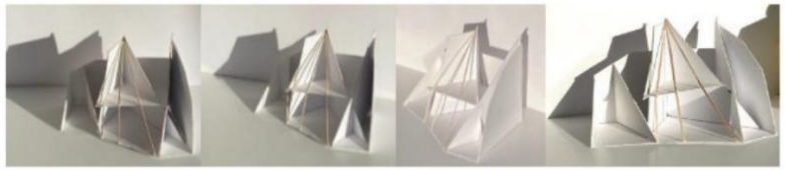


# Proposal – Final Hand Made Model


PROPOSAL - final design modelling 1:100

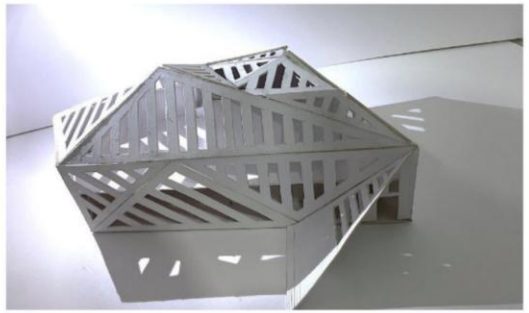


For my final proposal, I thought that my initial floor planning was too simple, so I decided to incorporate a tempered glass indoor parkour chamber that can be accessed through sliding glass doors on both the ground floor and first floor. This way the parkour can be showcased throughout the building and people can observe through the cafe and the main skating area on the ground floor. I felt that this feature not only combines characteristics of the use of glass in the 'Falkestrasse' but further implies my touchstone of creating a piece of architecture that has been seperated and put back together. I also decided to include a wall that also acts as shade and shelter from rain in the main enterance that is also skateable. Taking inspiration from the skate-park like shape of the 'The City of Culture of Galicia' I incorporated a skateable wall where fellow skaters can do a few tricks on. This not only showcases the talent of the skaters (showcasing the purpose of the building) but also conveniently links to the Tram Line Spot Skatepark where skaters can combine the two facilities, resulting in an even larger skatepark.



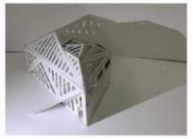

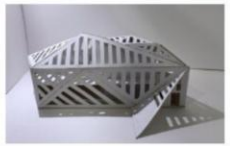


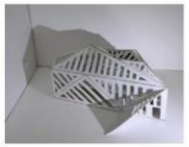







PROPOSAL - final design modelling on site 1:100

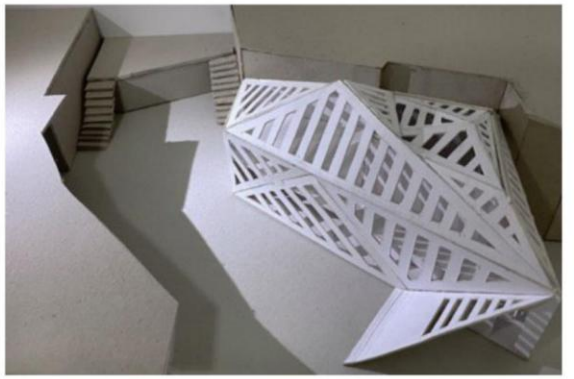



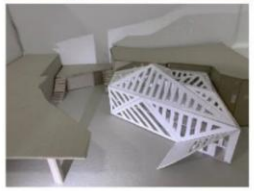



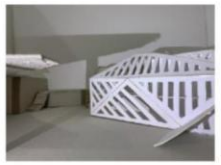











# MODULE:
# DESIGN STUDIO PROJECT 2

# Primer Project – Calmness within Chaos

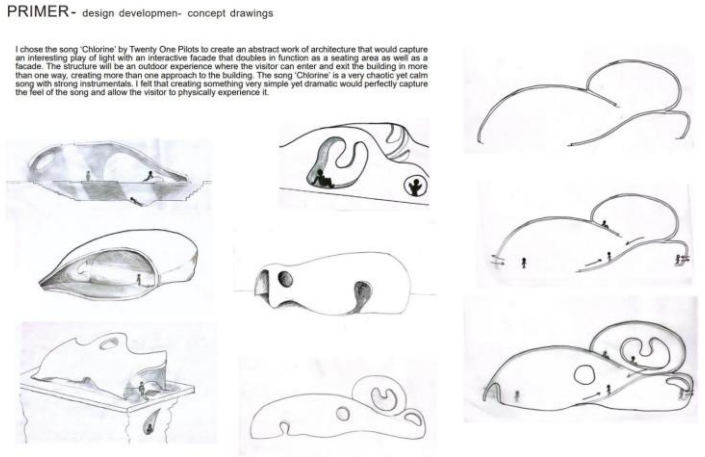

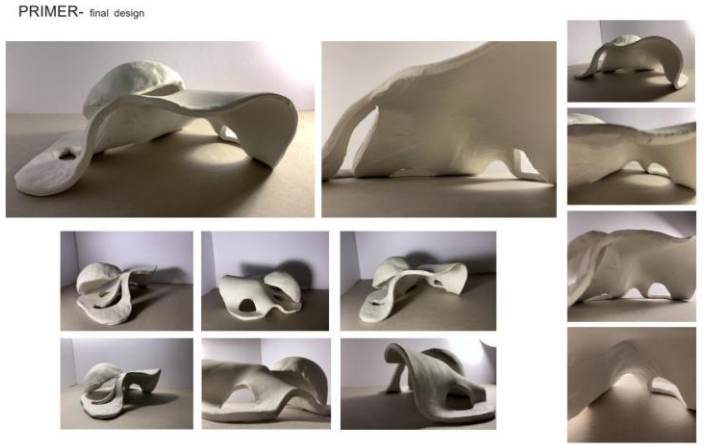




This primer project explored the relationship between music, light and architectural form, using Twenty One Pilots' Chlorine as a conceptual starting point. Through the design of an abstract, interactive structure, I experimented with the interplay between light and shadow, facade and function, and movement through space. The project introduced the idea of **calmness within chaos**, exploring how a simple yet dramatic architectural form could translate the contrasting moods of the song into a physical experience. This initial exploration established a conceptual foundation that would later develop further in my subsequent design work.

# Site Sketches + Plan

## Site Visits - NOTES AND ON-SITE SKETCHES


St. Mary's Rest Garden : Site notes (CHOSEN SITE)
→ Private / hidden
→ Sun is blocked by surrounding context, buildings
→ Evening light emerges more, grass / path / shaded couple
Lighting - not harsh on eyes
→ No wind reaching site, no breeze - even warmer on
warmer days
→ Access to site is limited / hidden, only a gate and
small pathway leading using between surrounding buildings
→ Secure area, site is boxed off, only 2 entrances
→ Sound wise it is quiet, calm due to no main
road and being closed off by context
→ Fence surrounding site = more private / safe / protected
→ Lace Market - Church nearby about hosts industrial
heritage
Broad Street : Site notes
→ car park, bus stop
→ in front of a night club / Pizza
→ Site at a slight incline
→ Lower pavement space
→ Loud, especially at night due to clubbing events @ Rogers
Brewhouse Yard : Site notes
→ Peace : Good for privacy, minimal noise
→ Historical Site : context interesting → Jerusalem Pub
(1883 when built)
→ But only as Site to close visits : historical attraction to Nottingham for tourists
→ 2 points of entry to opposite Wind Rose house, chimney stack
1 - by Sneinton Rd
2 - on castle boulevard
Duke's Place : Site notes :
→ Noisy because there is a stadium and a main road
→ very visible from the main road, there are only
trees and a foot path between the road and the site
→ Townhouse yard in terms of access
→ Historical Walk
→ very noisy as crowds / games on the arcade, Stadium
to the South and busy at match times
→ Leading from the Stadium Side
→ Level change (incline) of site
→ Lack of privacy


St. Mary's Rest Garden

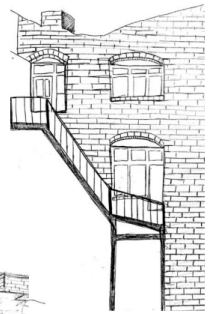
Broad Street


Brewhouse Yard

Sketchbook Drawings

1 Derin Enhos
20481498

## Site Analysis - Site Plan 1:500




## St Mary's Rest Garden - CHOSEN SITE SKETCHES











Sketchbook Drawings

1 Derin Enhos
20481498

## Site Analysis - Chosen site, photos, brief

**Chosen Site:** SITE C, St Mary's Rest Garden
**Chosen Brief:** Brief 01, Early Years Development Hub
**Client:** A funding partnership between Nottingham City Council, the Royal Foundation, Nottingham College and the University of Nottingham is the client for the project.



2 Derin Enhos
20481498

# Site Sections + Elevations – Hand Drawn

Site Analysis - Site Sections

Section C-C - 1:250




Site Analysis - Site Sections

Elevation B-B - 1:250





Site Analysis - Site Sections

Section A-A - 1:250




# Site Analysis

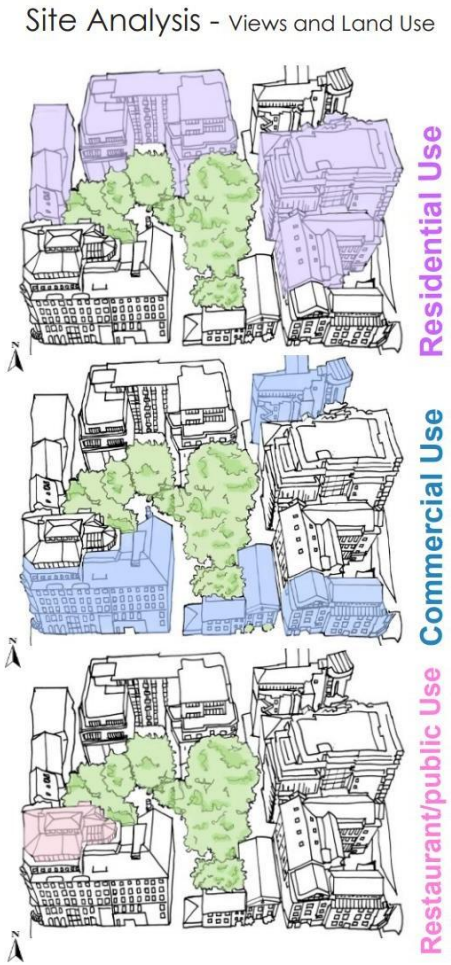






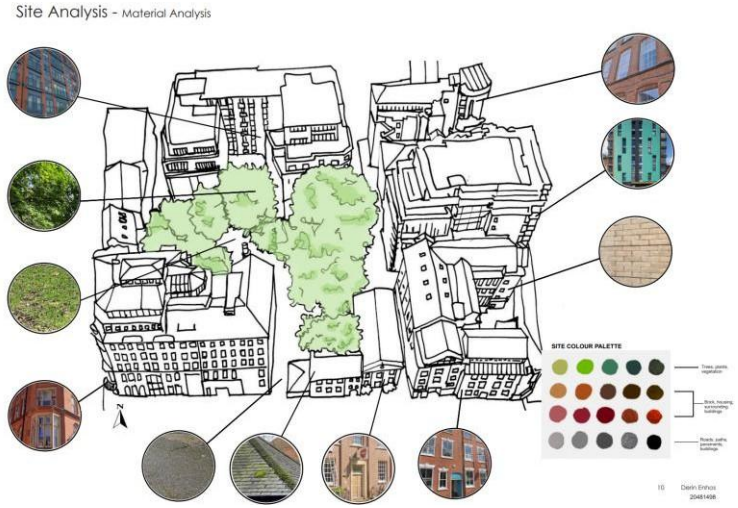

# Spatial Sequence

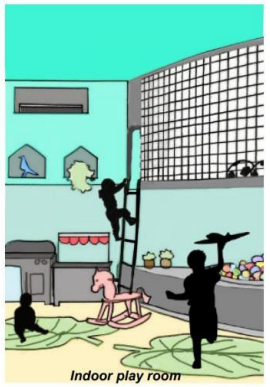

Indoor play room



Student study space



Sheltered outdoor play area (courtyard)



Cafeteria




Sensory room



Sheltered outdoor play area (courtyard)



Consultation room

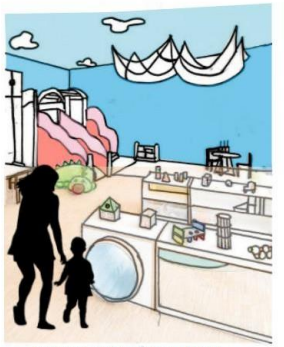


Classroom (educational play)

Drawings of different rooms in the Children's Centre.

# Calmness within Chaos

## Calmness within Chaos - Concept

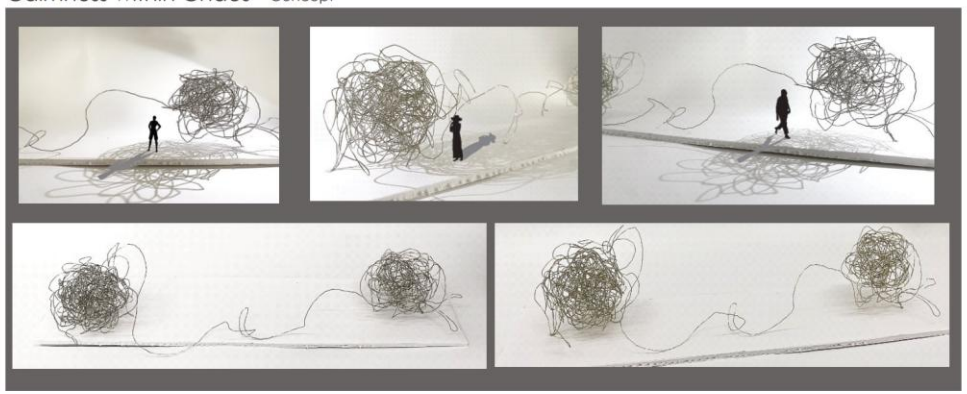




The concept of entering a private, secluded place within the chaotic nature of a busy city and experiencing that sudden feeling of peace. A zen that takes form in a secret garden in the middle of the city centre, finding calmness where you least expect it. Having the tranquillity consume you rather than the hectic essence of a city. Inspired by Jimmie Durham's artwork titled 'Our House'.





## Design Process - Sketches

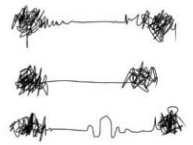

Going from concept to building




This drawing reminds me of two buildings with either a bridge or pathway linking the two.




Concept to idea




In the shape of the site, pathway in between

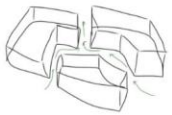


3 building in blocks, passageway through it

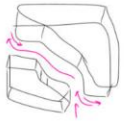


2 building in blocks, passageway through it

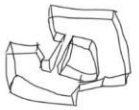



2 building in blocks, passageway through it with access via overhead bridge

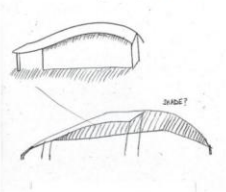

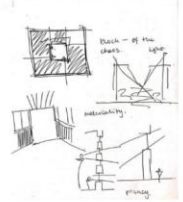


# Design Process + Iterations

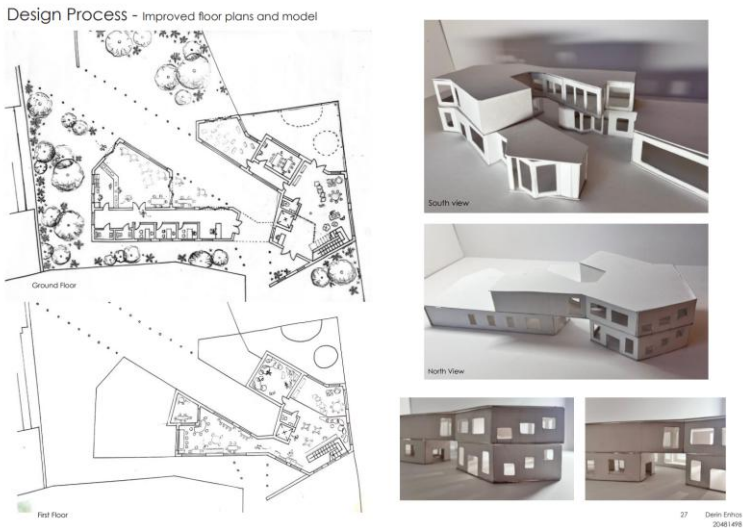

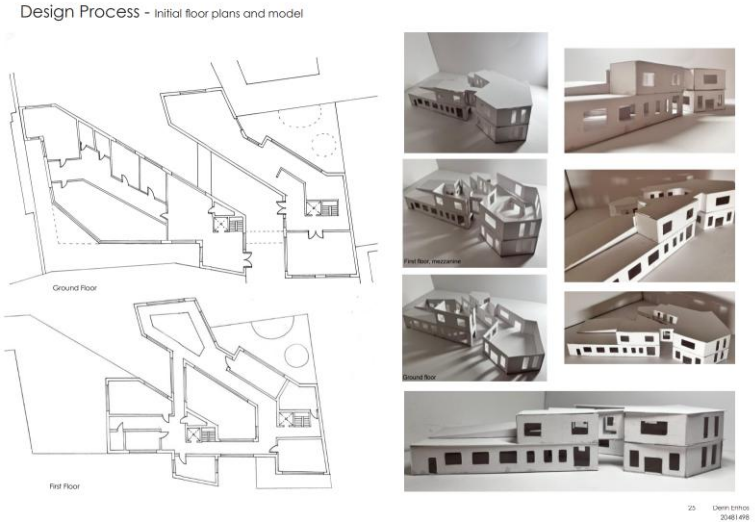




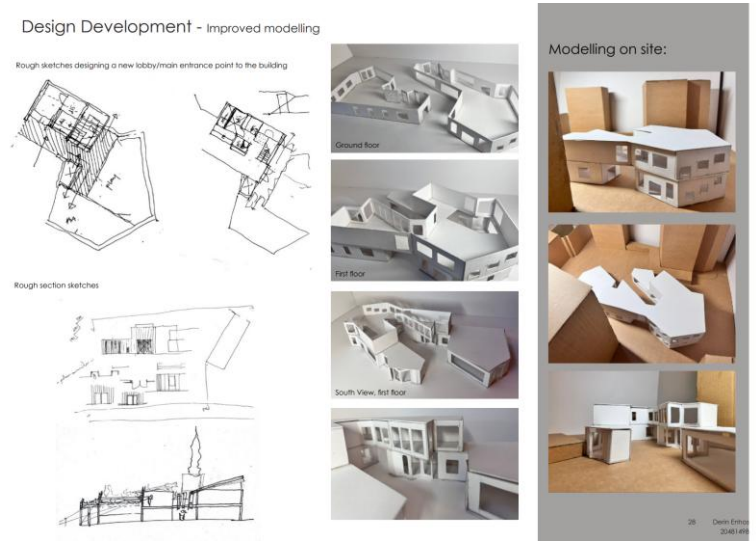


# Final Floor Plans + Sections – Hand Drawn


Ground Floor Plan - 1:100

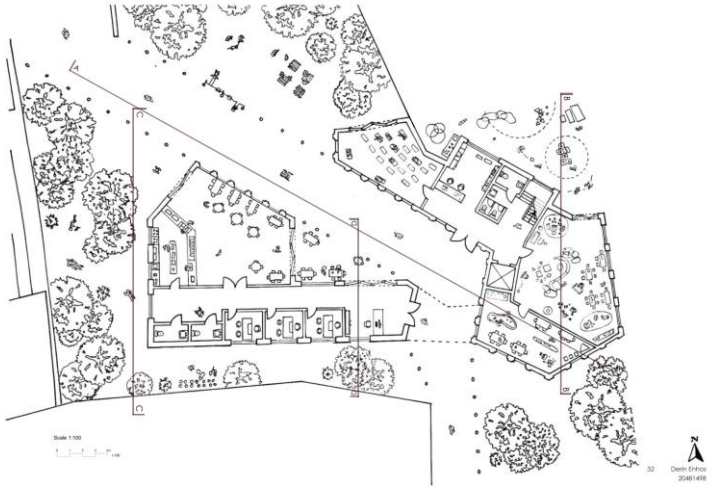

First Floor Plan - 1:100

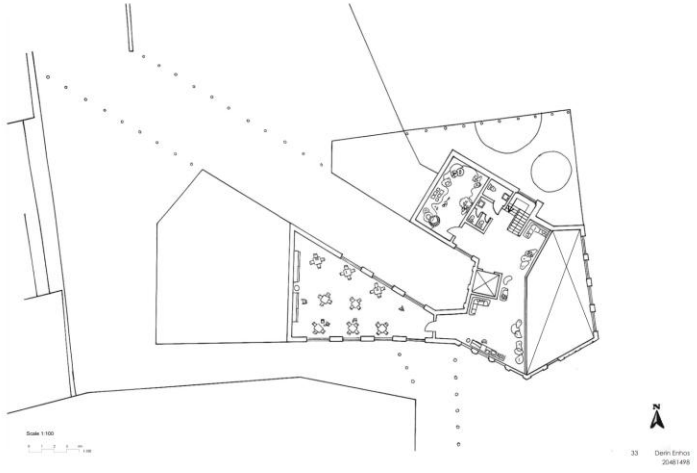

Sections A-A, B-B - 1:100

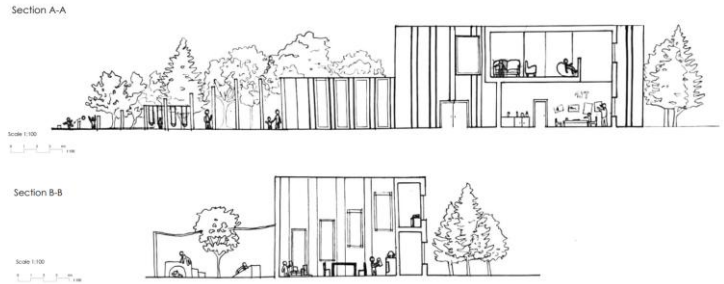


# Final Model – Hand Made

Final Model


North view


South-west view

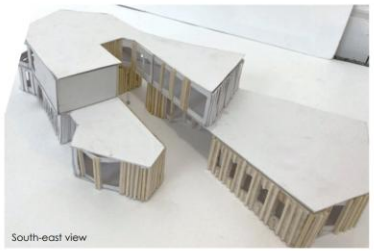
South-east view


North-east view





Final Model on Site



Final Model - Close ups


Walk through



Entrance, overhead bridge


Outdoor cafe





Mezzanine



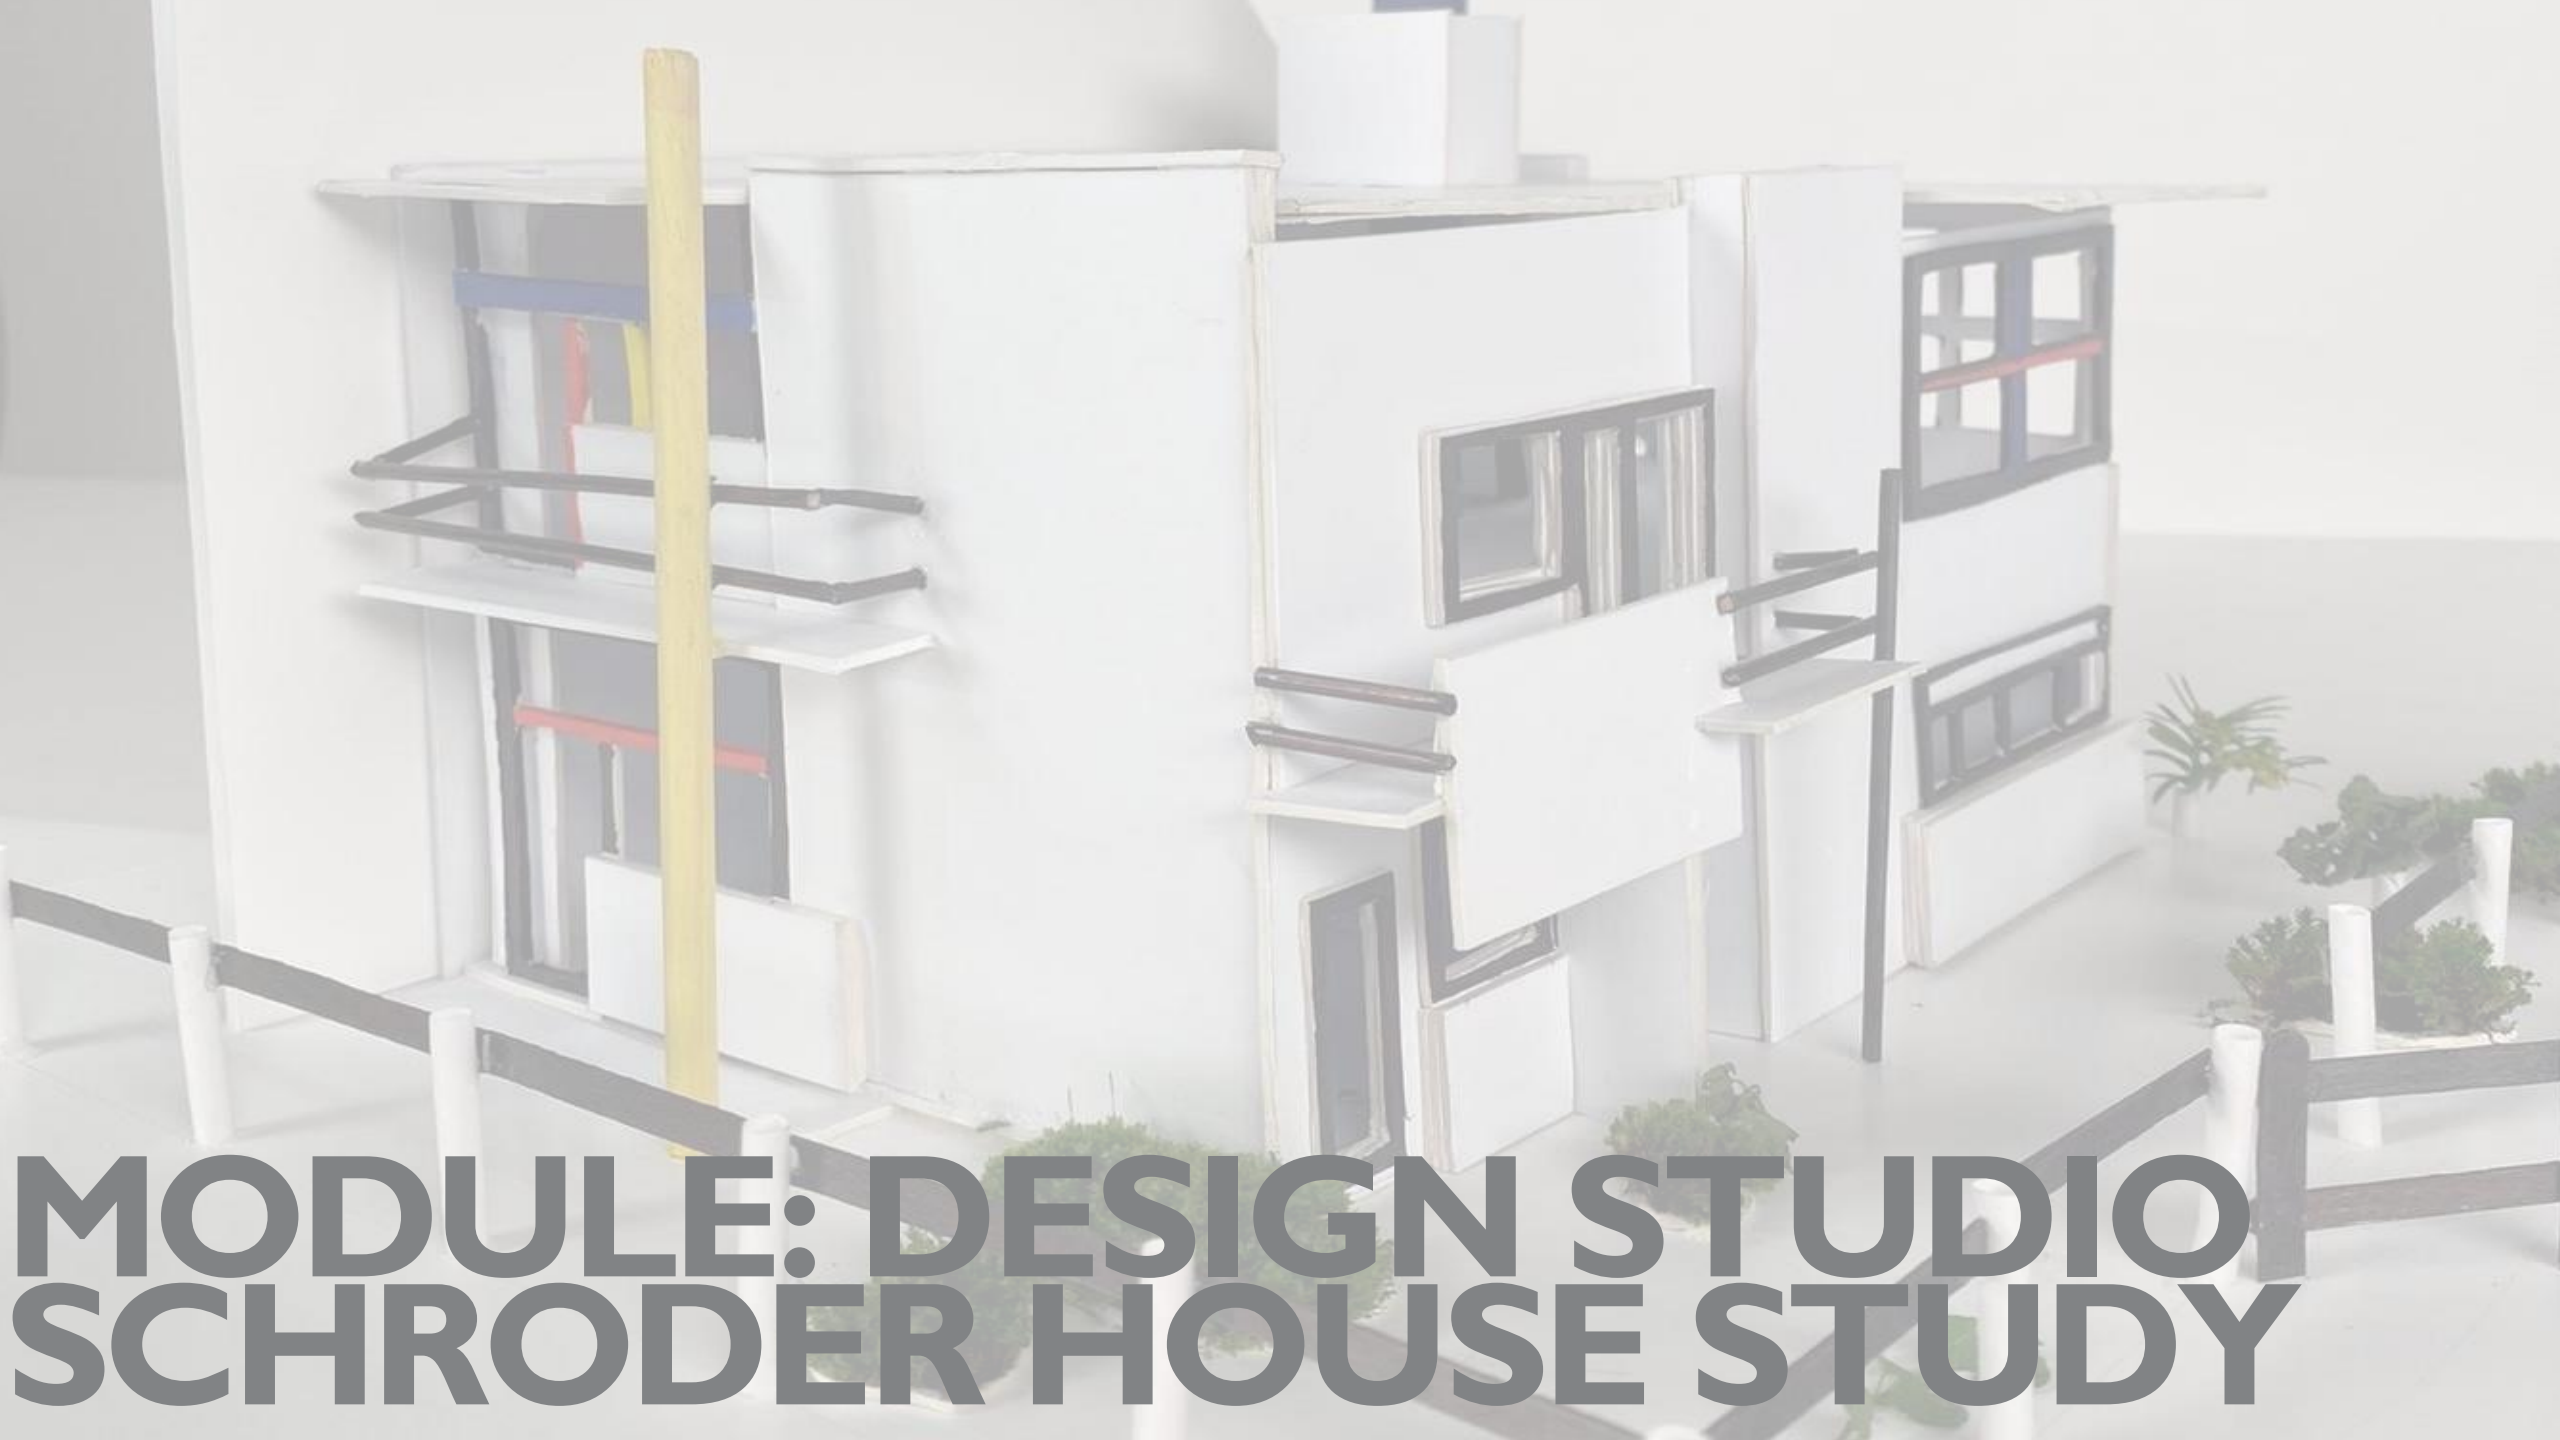


# MODULE: DESIGN STUDIO
# SCHRODER HOUSE STUDY

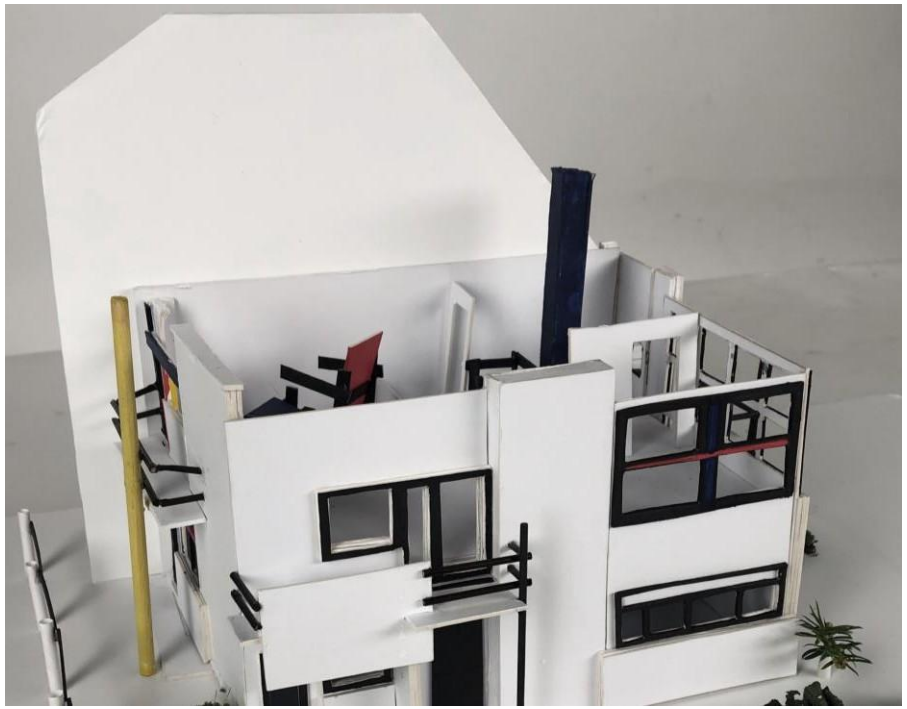








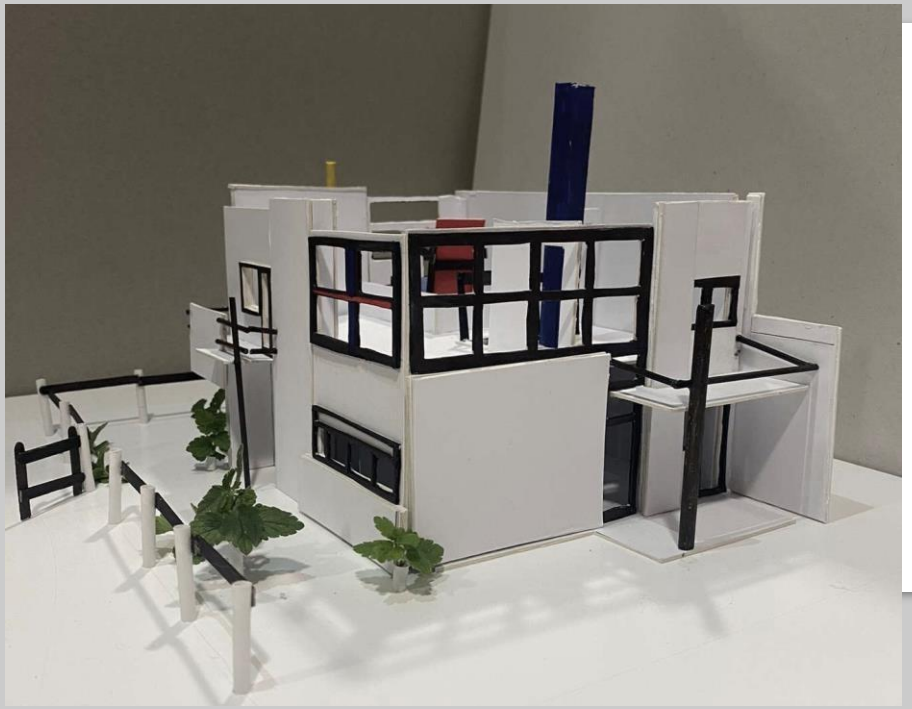




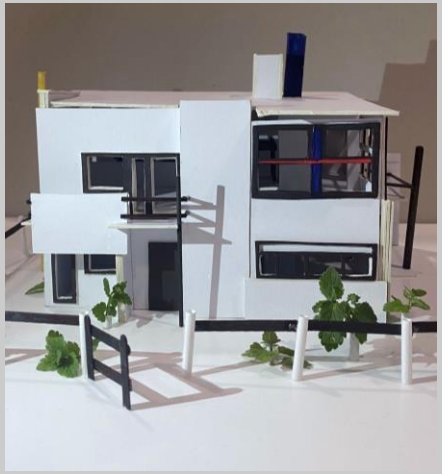





## Schroder House - Elevations

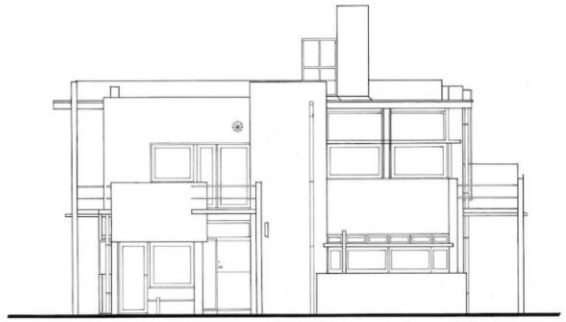

Front elevation (southeast)

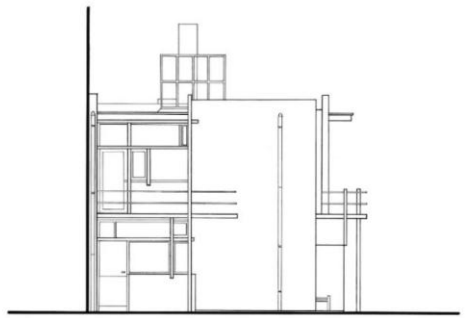


Side elevation (southwest)

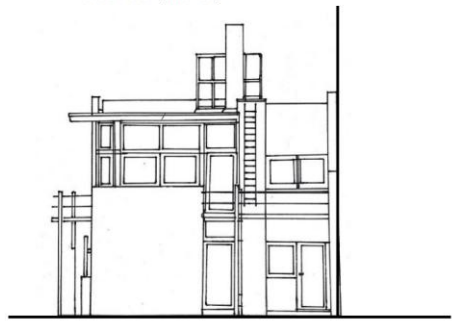

Side elevation (north-east)

## Schroder House- Final Model

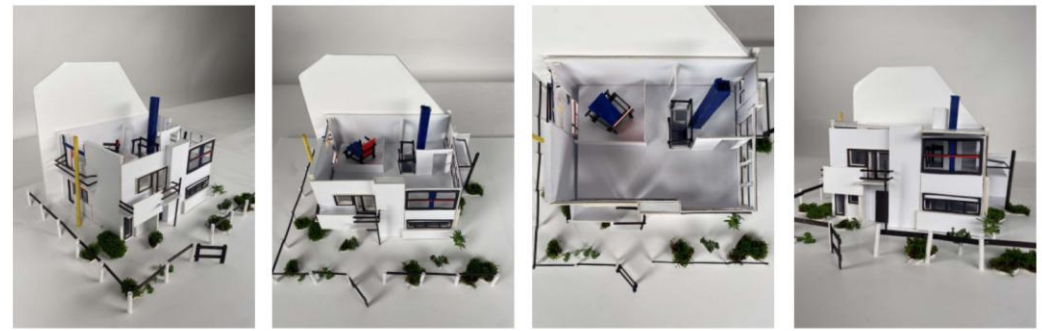




Front elevation (southeast)

Side elevation (southwest)

Side elevation (north-east)

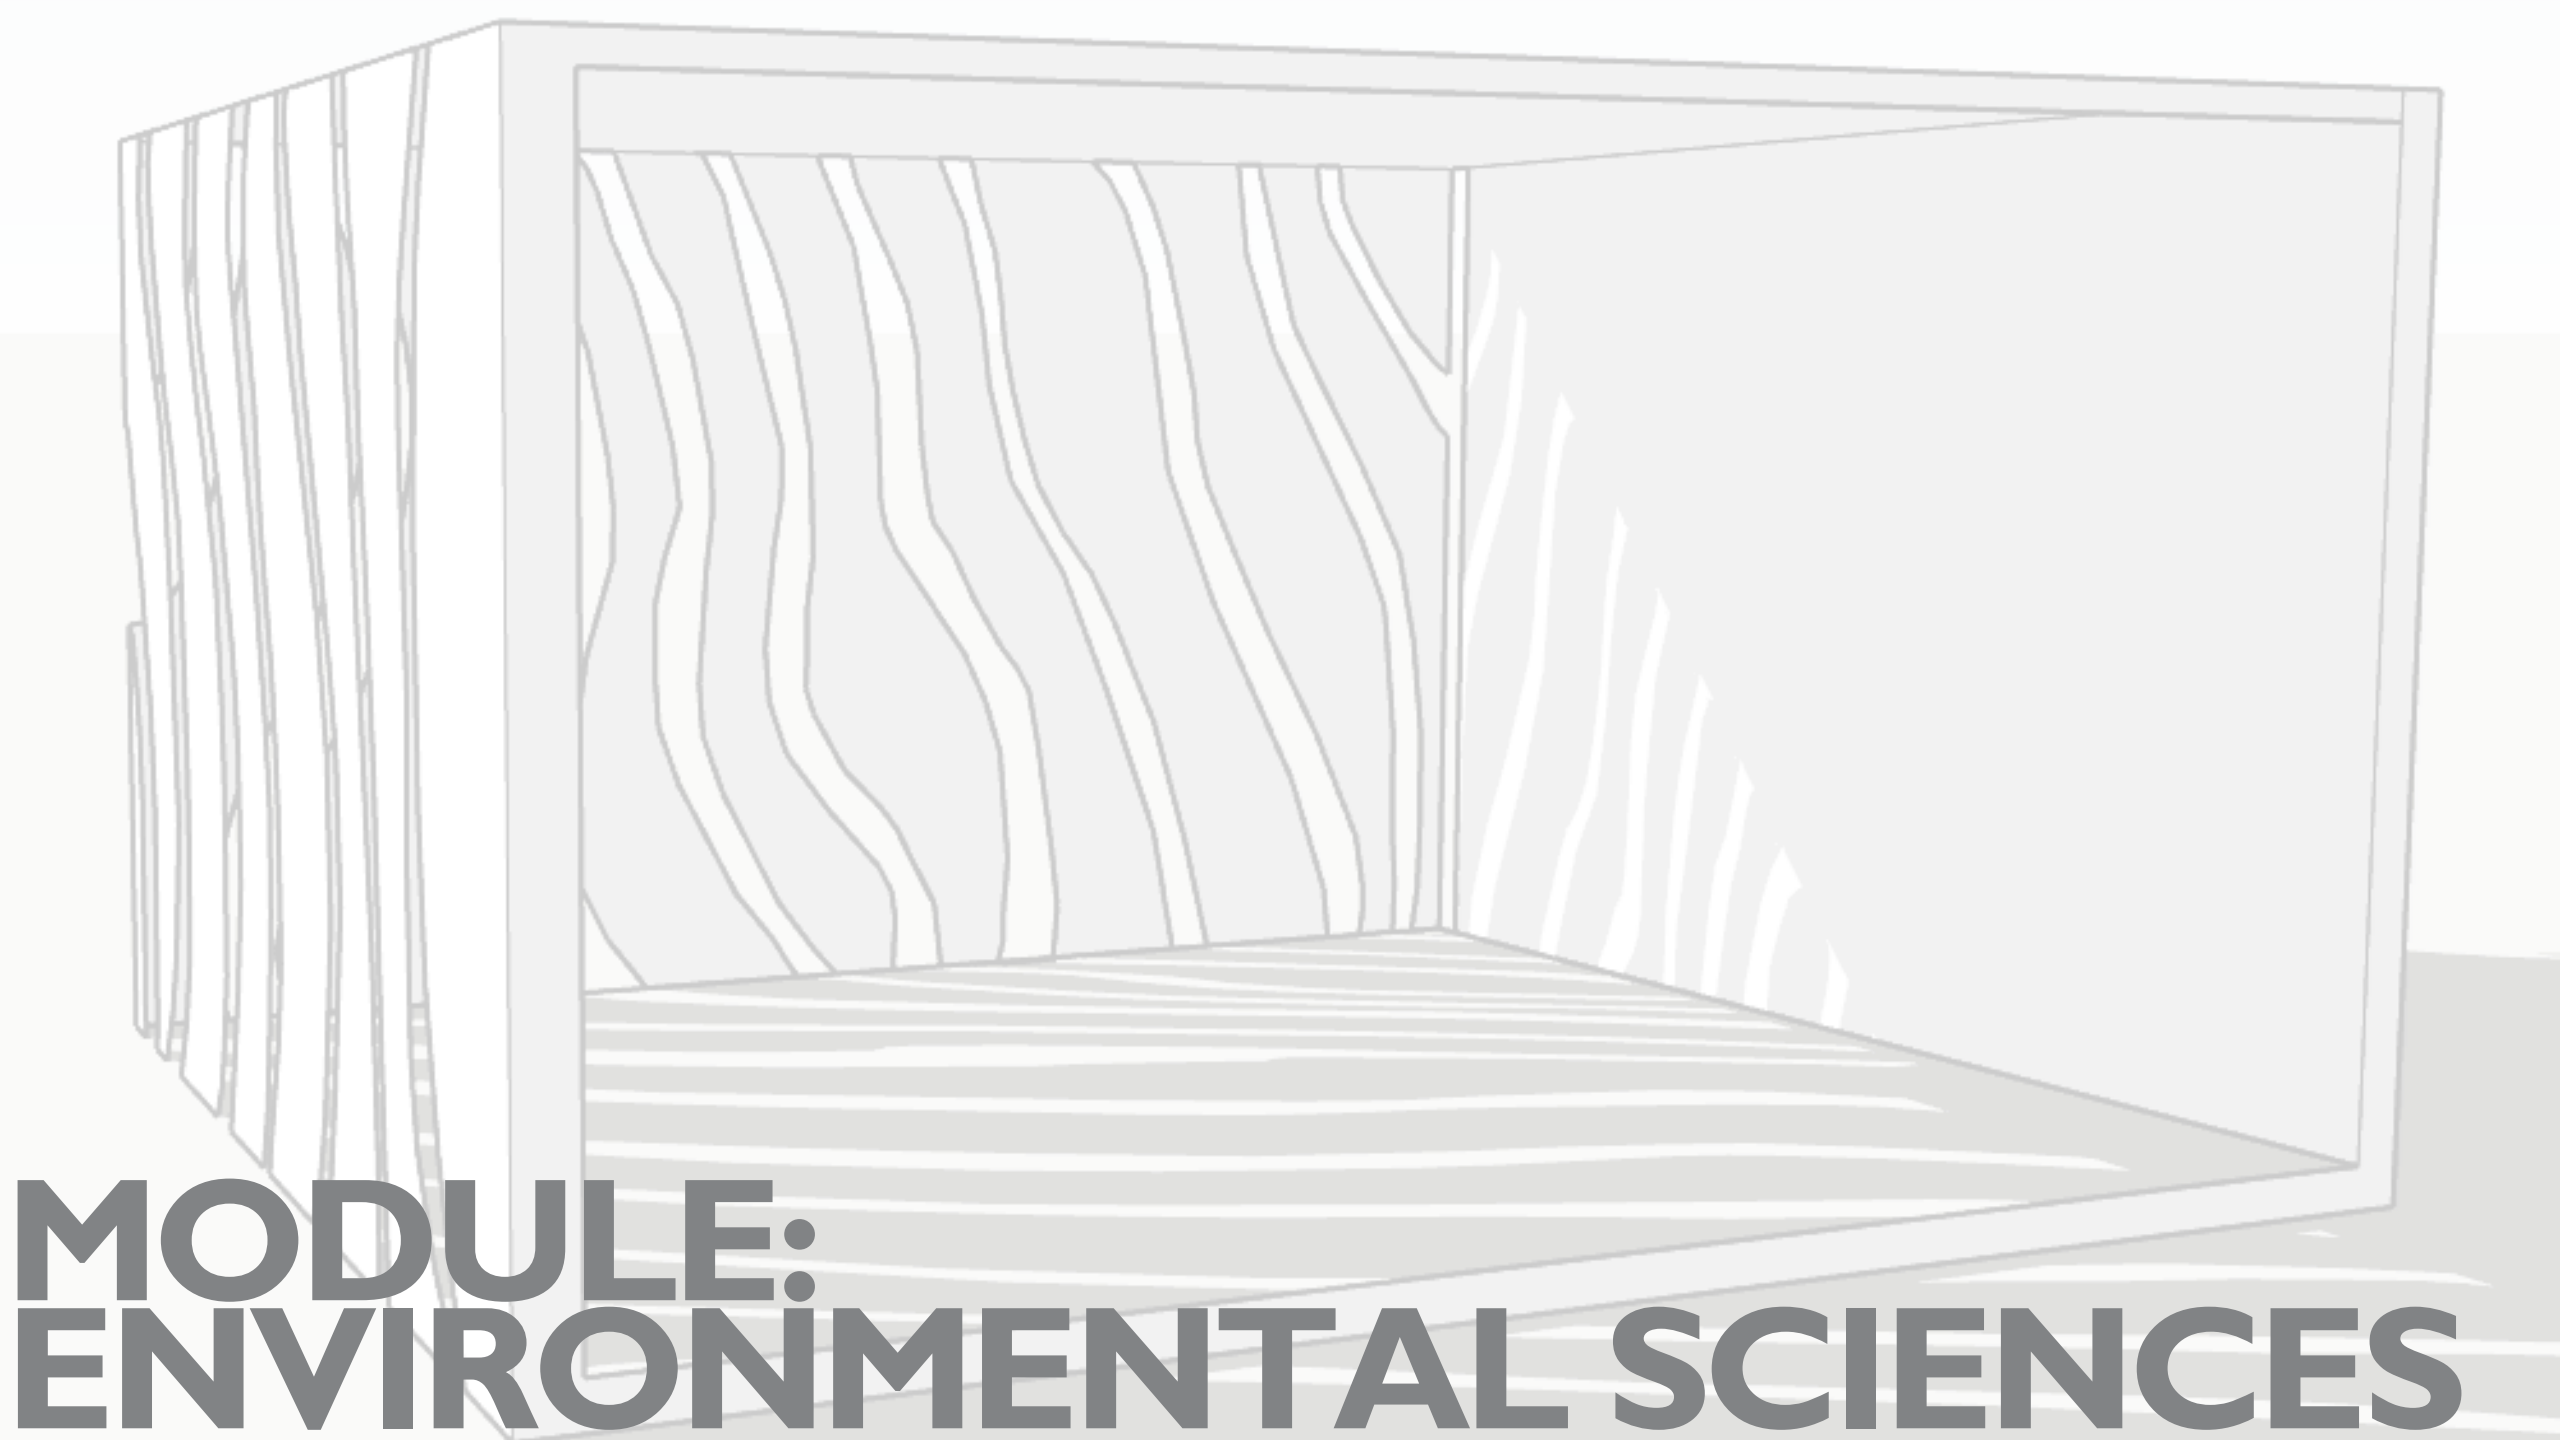

# MODULE: ENVIRONMENTAL SCIENCES

# Broad Museum Façade Experimentation

Conducting a comprehensive analysis of the facade of the Broad Museum with the aim of conceptualizing and
designing an innovative replacement.

## Design Experimentation



*Diffusion of light with a singular façade + ceiling*



*Diffusion of light with a singular façade + rotating the ceiling*







*Figure 46 – Photograph showing how the continuation of the irregular façade to the ceiling adds more slits of light*

## Façade Experimentation – Testing different cut-outs



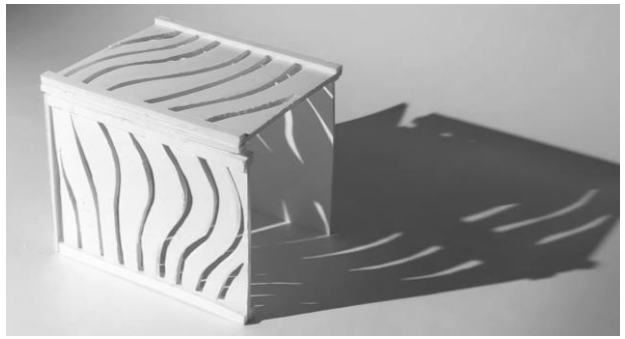
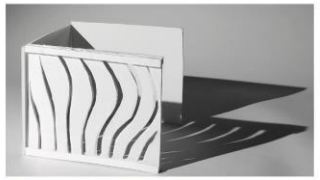


*Figure 32 & 33 – Abstract cut out for a more dynamic-looking facade*






*Figure 34 & 35 – Shows the type of shadows created indoors at 2 different angles*
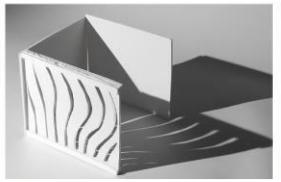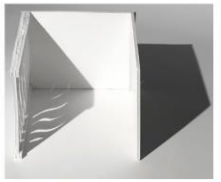
## Façade Experimentation – Testing a double façade




*Figure 37 – A double facade*

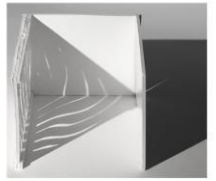


*Figure 38 – Showing the thickness of the facade*

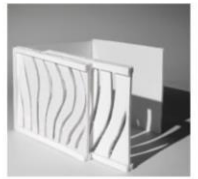


*Figure 39 – Play of light with 2 facades*

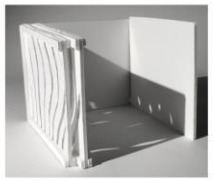


*Figure 40 – Blocking light*

As shown in Figure 40, the level of lighting is close to total blackout as the second slider is able to almost fully block all lighting. This can be useful for the hotter days in LA where the temperature is too hot to allow high levels of lighting in the building. Can be adjusted for user comfort.

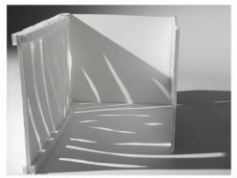

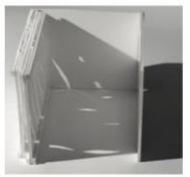


*Figure 36 – Photograph of how the abstract cut-out diffuses light.*





*Figure 41 – Shows how a double façade manipulates the diffusion of light, making it even more abstract.*

## Design Experimentation – Adding a ceiling

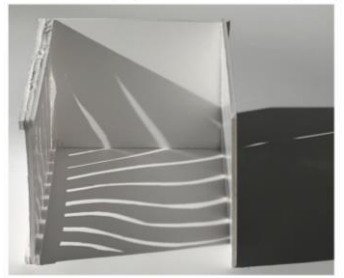

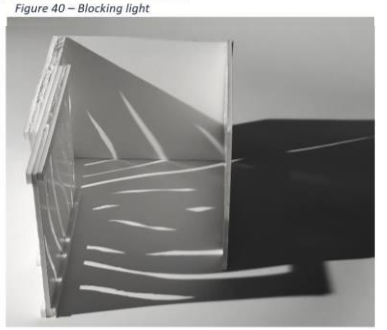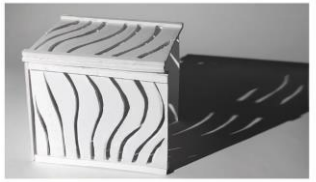


*Figure 42 & 43 – Addition of a ceiling to improve the play of light, and create more dramatic shadows and patterns of light*










*Figure 44 & 45 – Shows the diffusion of light*

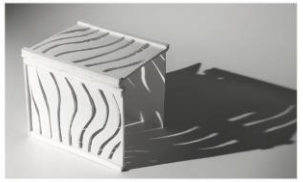
# Façade Experimentation – SketchUp Modelling



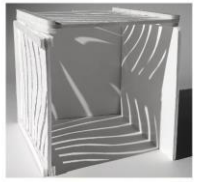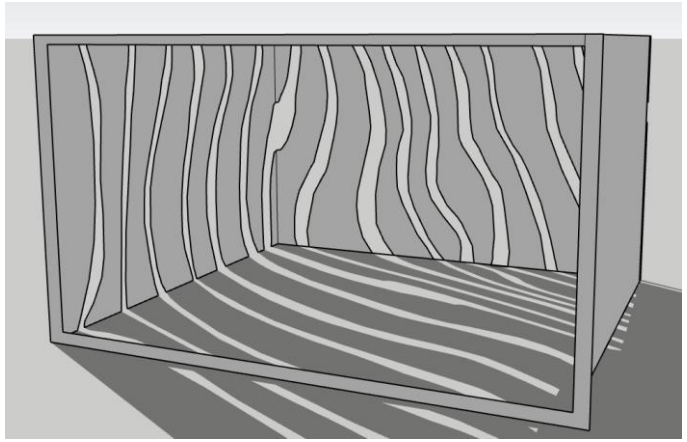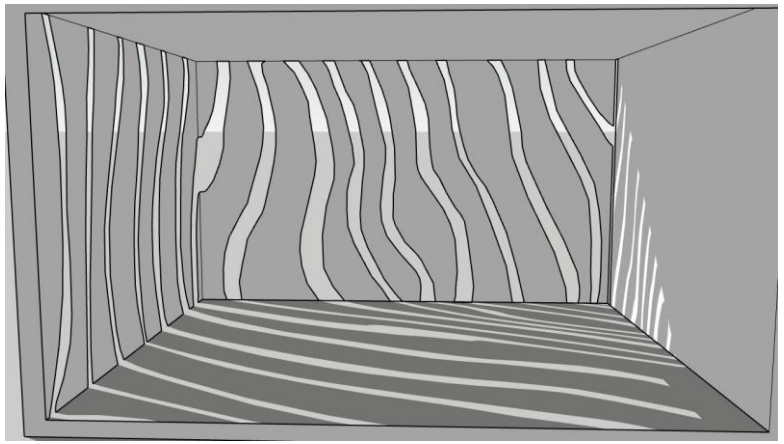

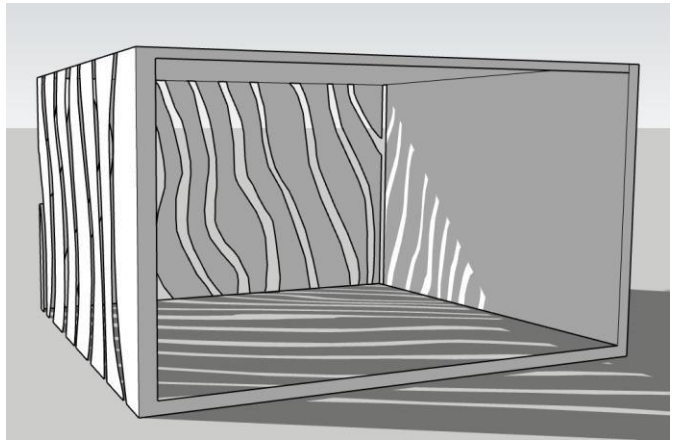


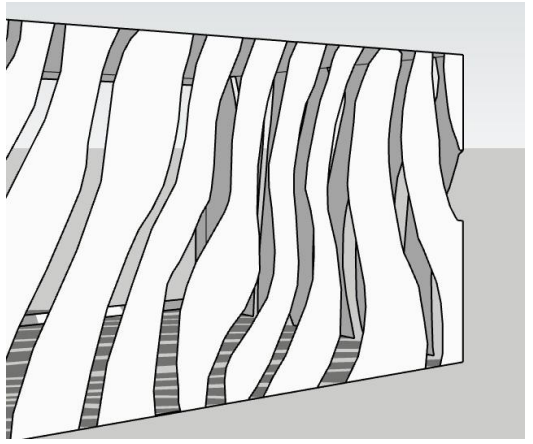


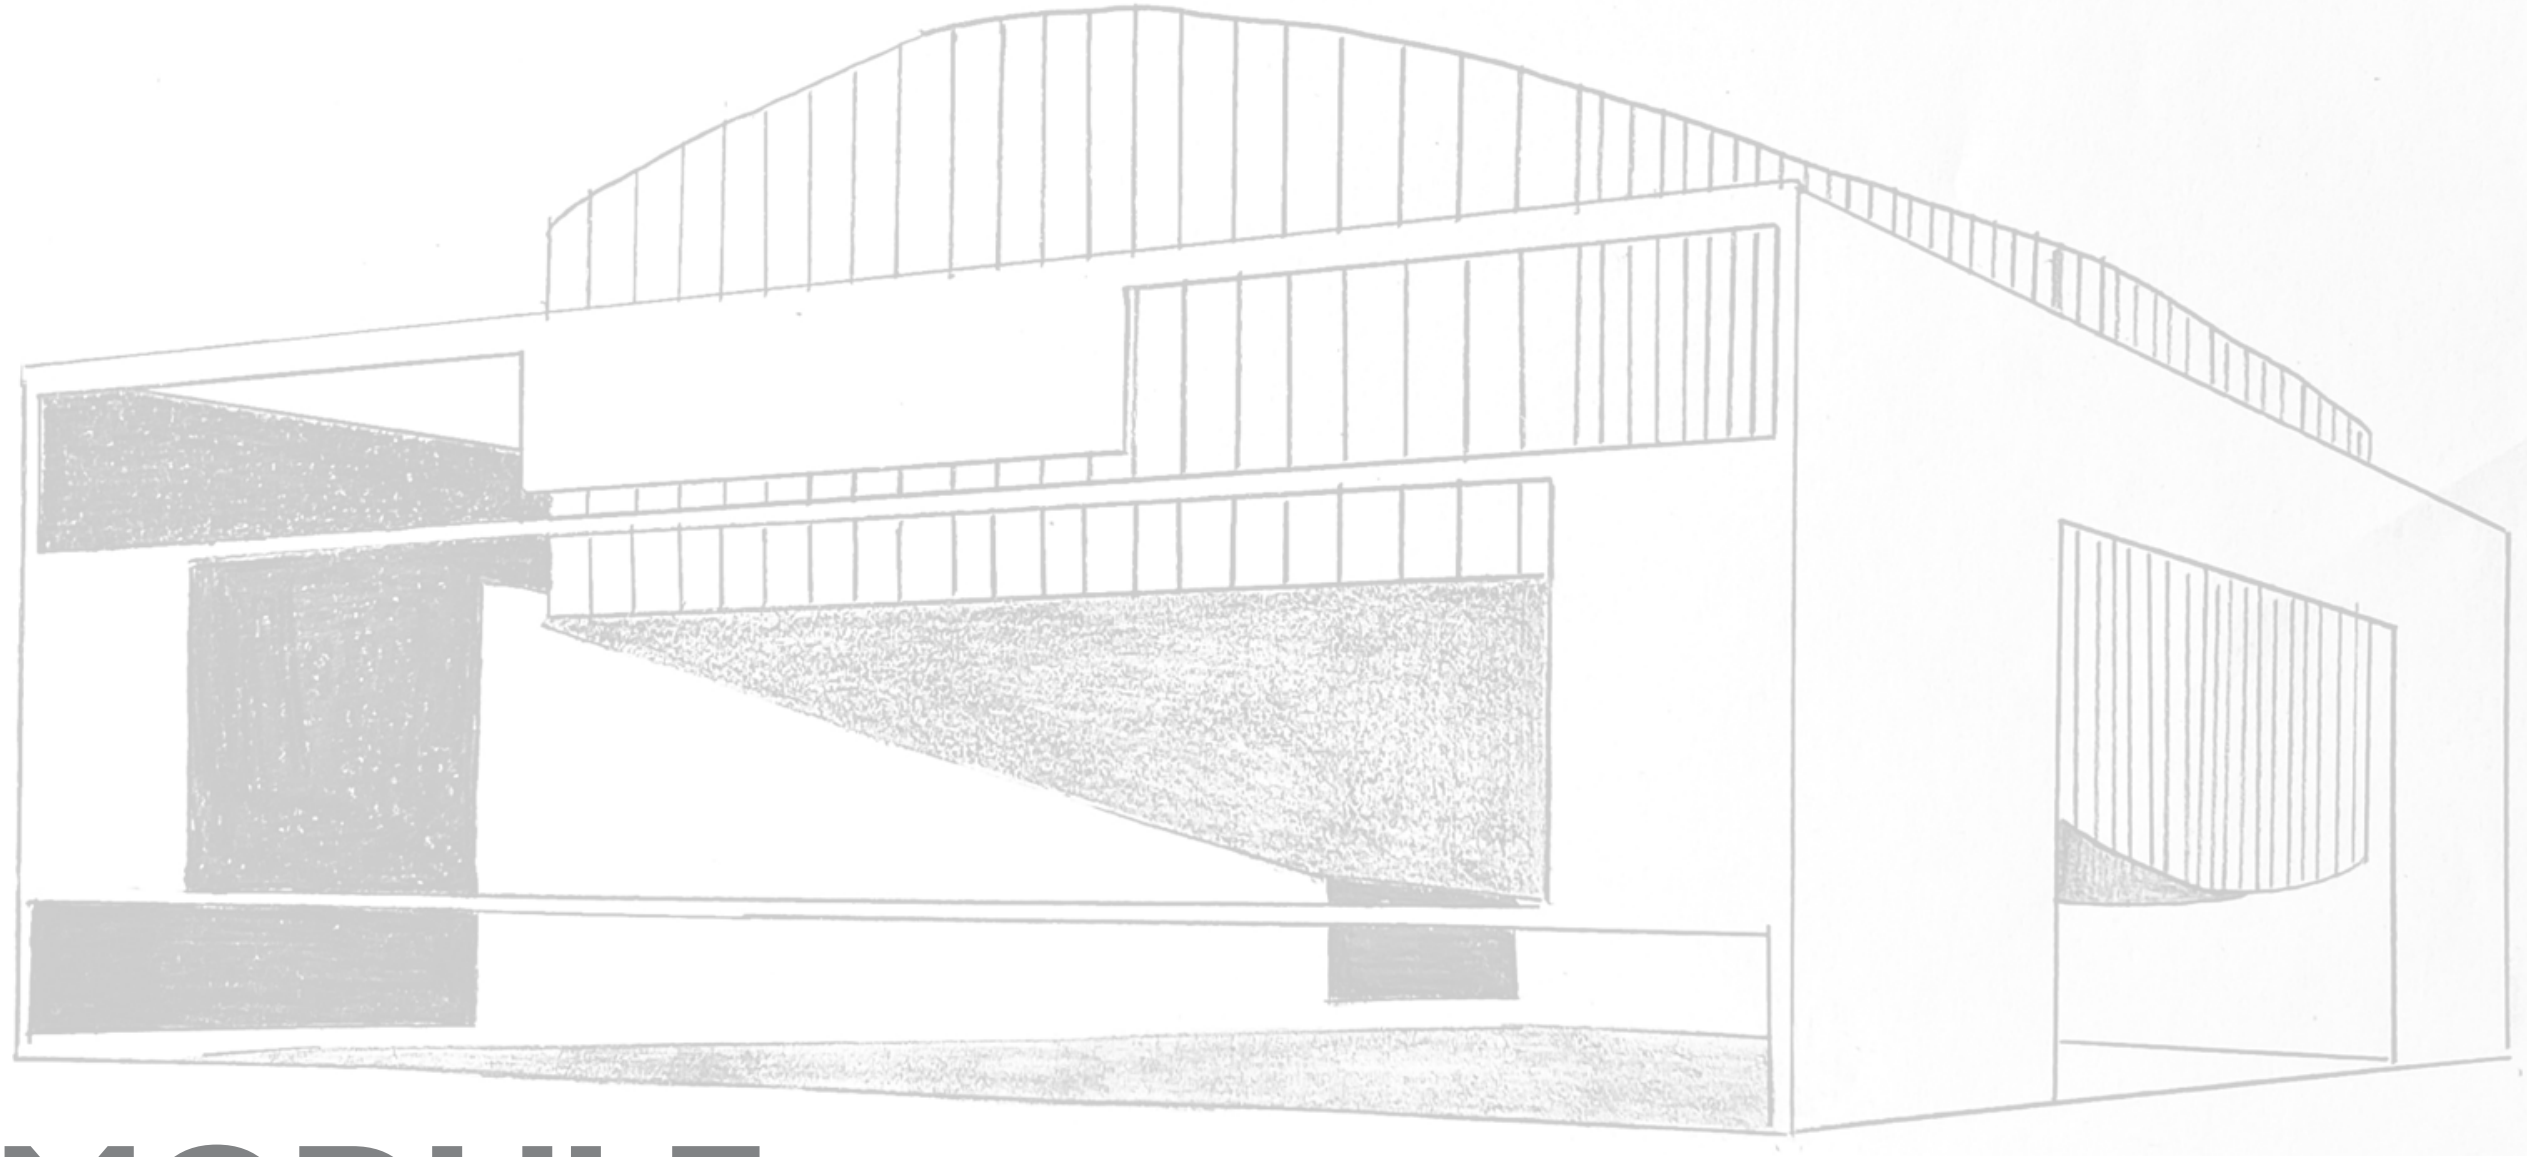


# MODULE:
# INTEGRATED DESIGN

# Royal Festival Hall, London – Study of Building Design

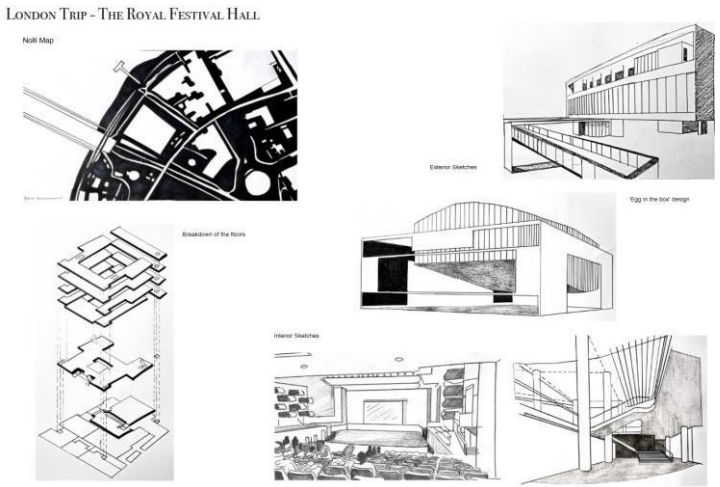


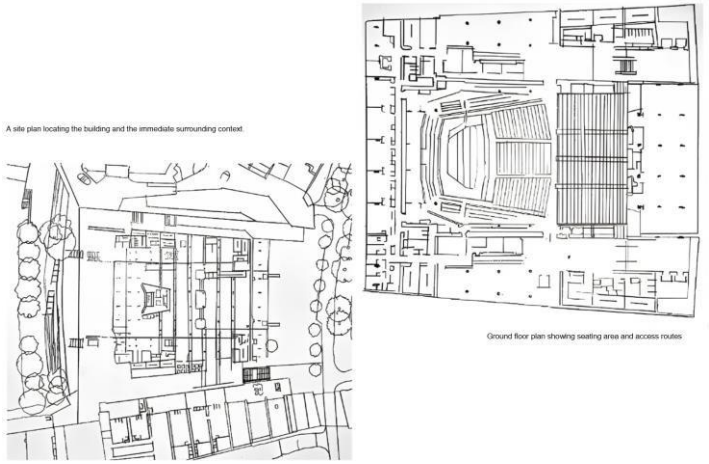
Embarking on a visit to the iconic Royal Festival Hall in London to conduct an in-depth analysis of its architectural design, meticulously examining its intricate plans and sections.
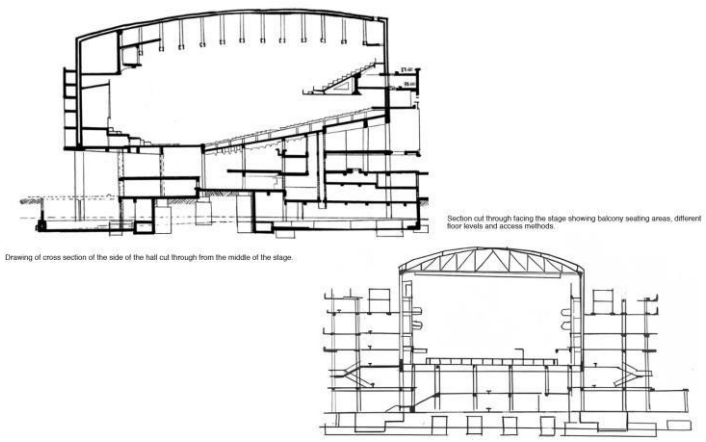
# MODULE: TECTONICS



## Tectonics Building Forensics
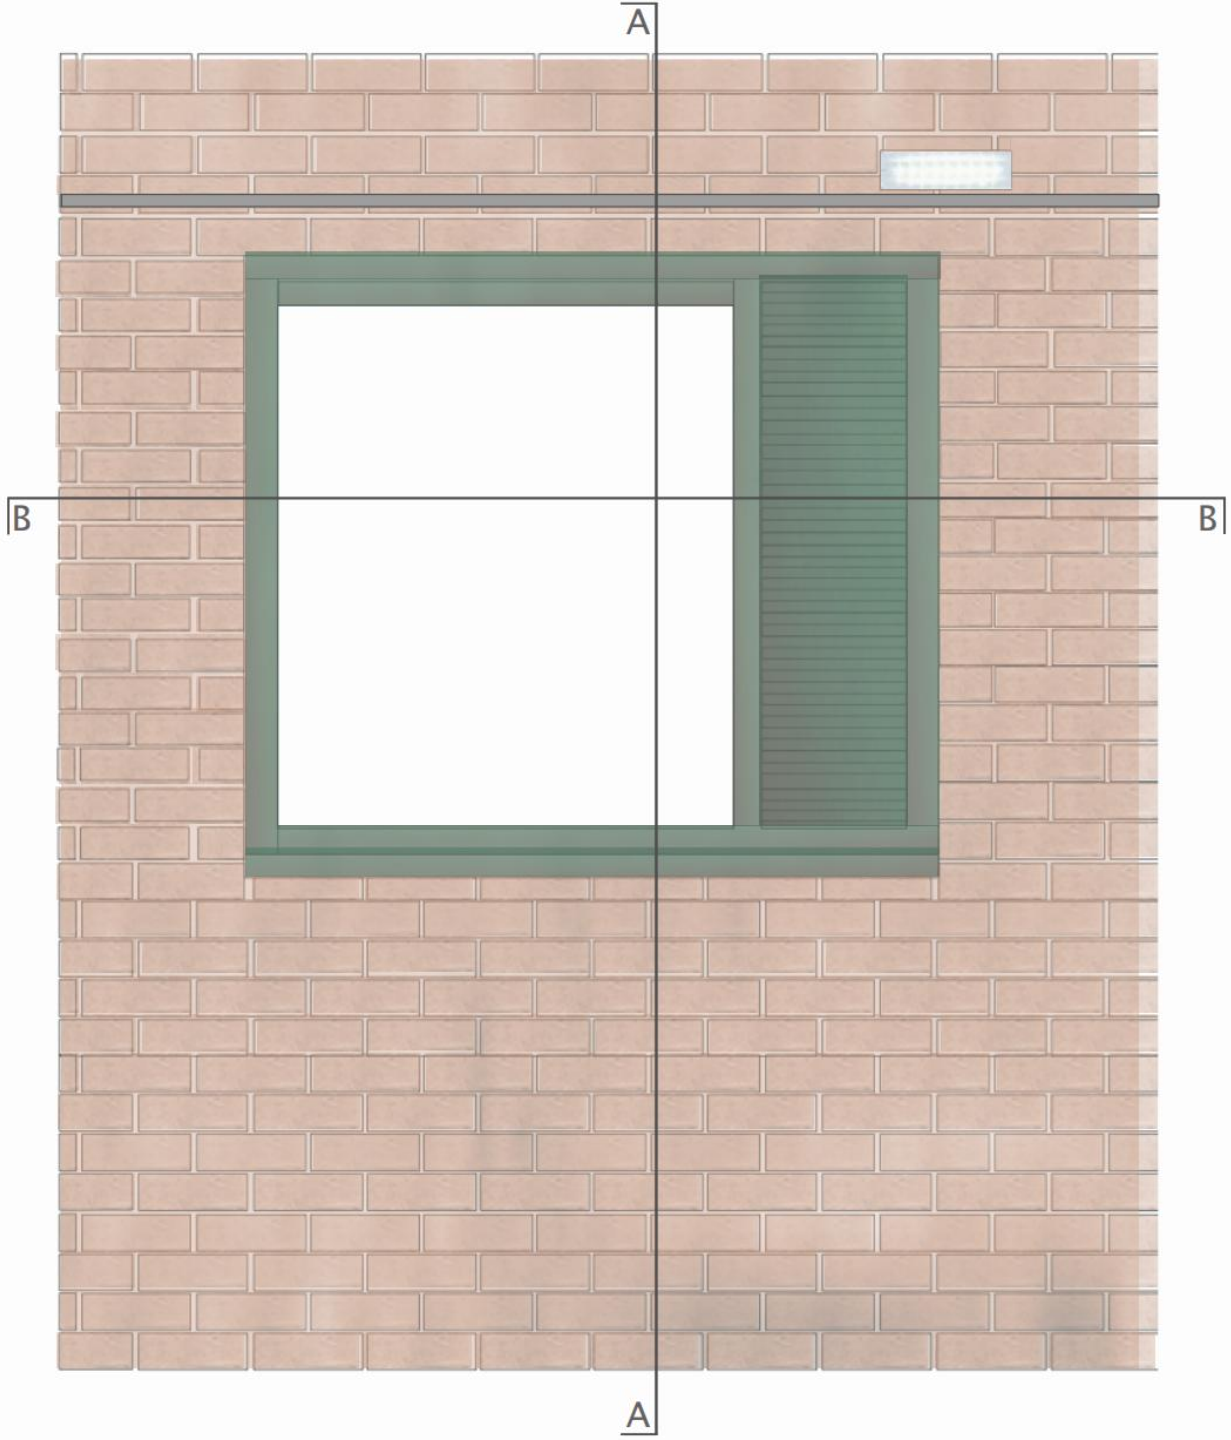
### Context




The opening I have chosen is one of the windows in the pantry of the EEC Studio.

Photo showing external view



Photo showing internal view

### Materiality Study

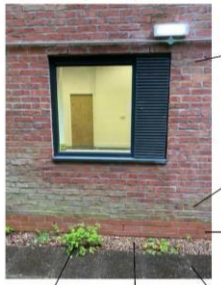



Traditional Red Brick

Matches the aesthetic of surrounding buildings.



The effect of weathering, the traditional red brick is stained green due to rain, moss, etc.



New Red Brick



Vegetation




Pebbles



Polished Tarmac Path

Studying the materiality of the opening in order to get a better understanding of its composition and components, aesthetic and functional purposes. For example, the polished tarmac provides a smooth look yet is still rough in texture to prevent slipping during rain.

### Components

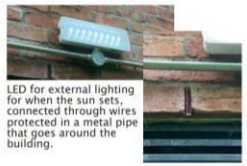

LED for external lighting for when the sun sets, connected through wires protected in a metal pipe that goes around the building.




Metal Window shutter

(Dark green)

## Working Drawings 1:10

Exterior Elevation 1:10

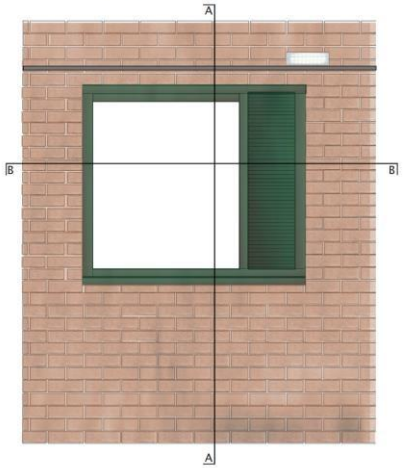



Section A-A 1:10



**Section A-A**

1. Double glazed glass
2. Cavity for double glazed glass (approx. 15mm)
3. Sealant fix around glass
4. Metal window frame (dark green)
5. Window frame
6. Exterior window cill
7. Interior window cill
8. Red outer brick
9. Mortar
10. Cavity wall
11. Insulation

Plan (Section B-B) 1:10

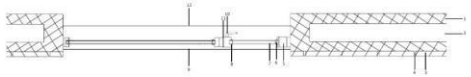

**Plan (Section B-B)**

1. Cavity wall
2. Insulation
3. Red outer brick
4. Mortar
5. Metal window frame (dark green)
6. Cavity for double glazed glass (approx. 15mm)
7. Double glazed glass
8. Sealant fix around glass
9. Exterior window cill
10. Interior window handle (with lock)
11. Sealant (watertight window close)
12. Interior window cill

Technical drawings of a window aimed at comprehensively illustrating its technical composition.