

ISTANBUL, TURKEY
July 2024 – Aug 2024

I-AM ASSOCIATES
INTERNSHIP


Research - Mood Board

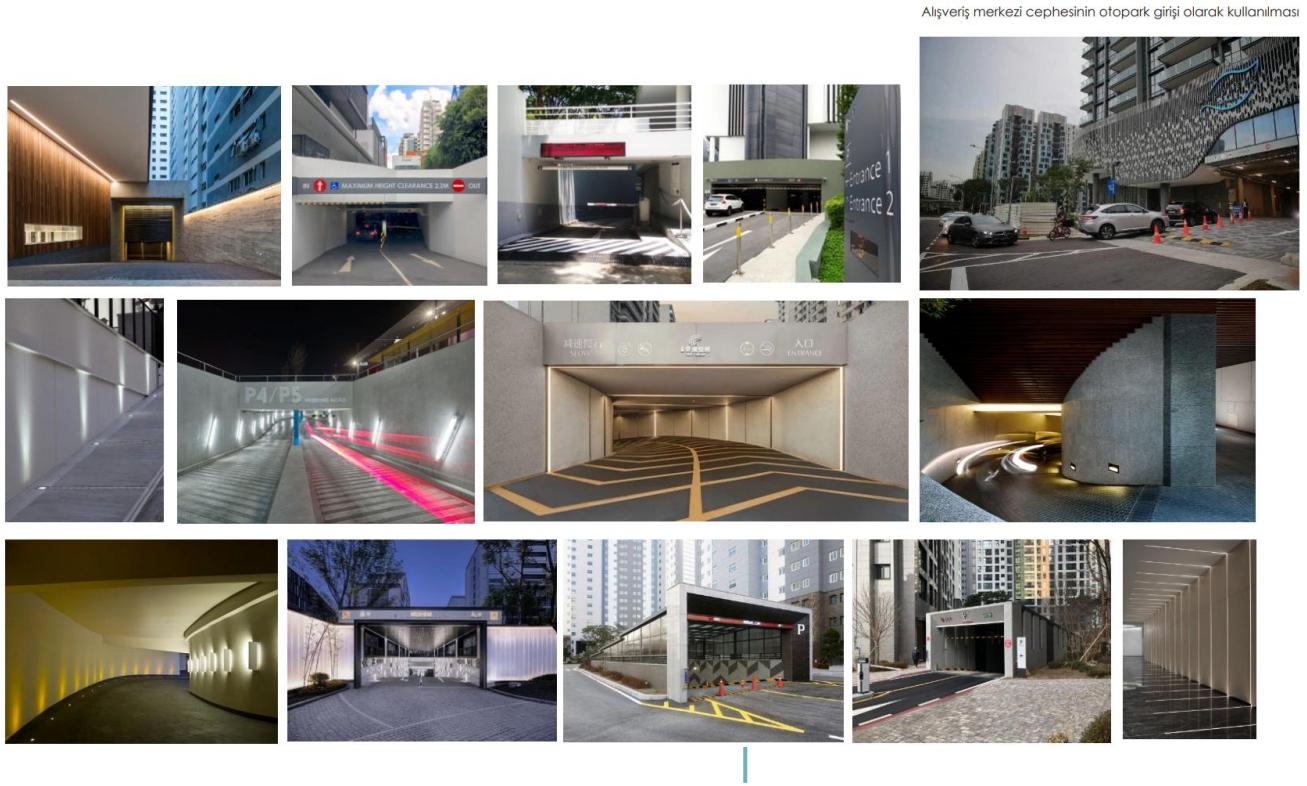

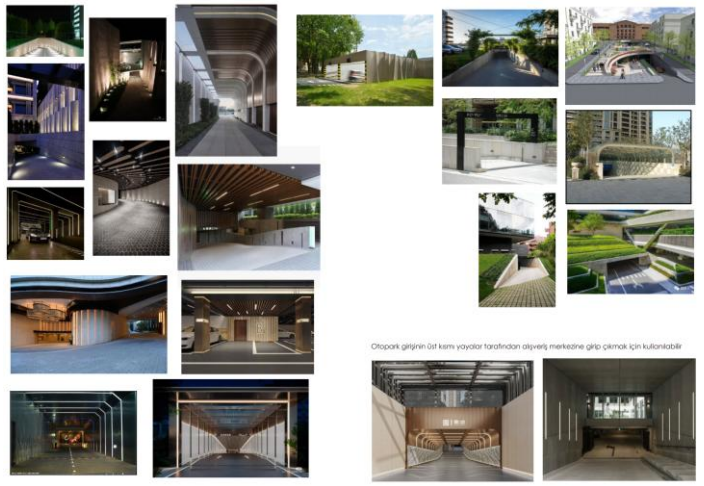


Full-time interior design intern, supported project teams in design development and client communication for a large retail redevelopment project. Used AutoCAD and SketchUp to finalize floor plans for a mall revamp project in Istanbul.

Final Floor Plan

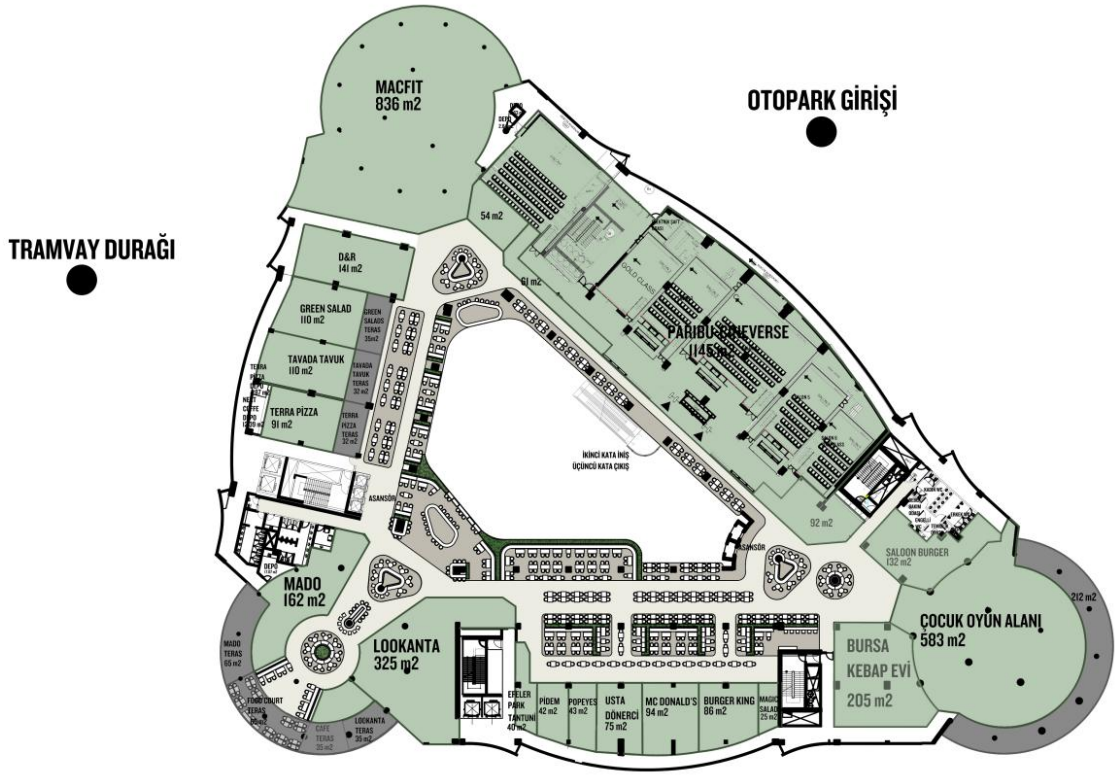

MAĞAZA: 4642 m2
KİOSK: 24 m2
KİRACI TERAS: 379m2


ISTANBUL, TURKEY
Oct 2023 – Dec 2023

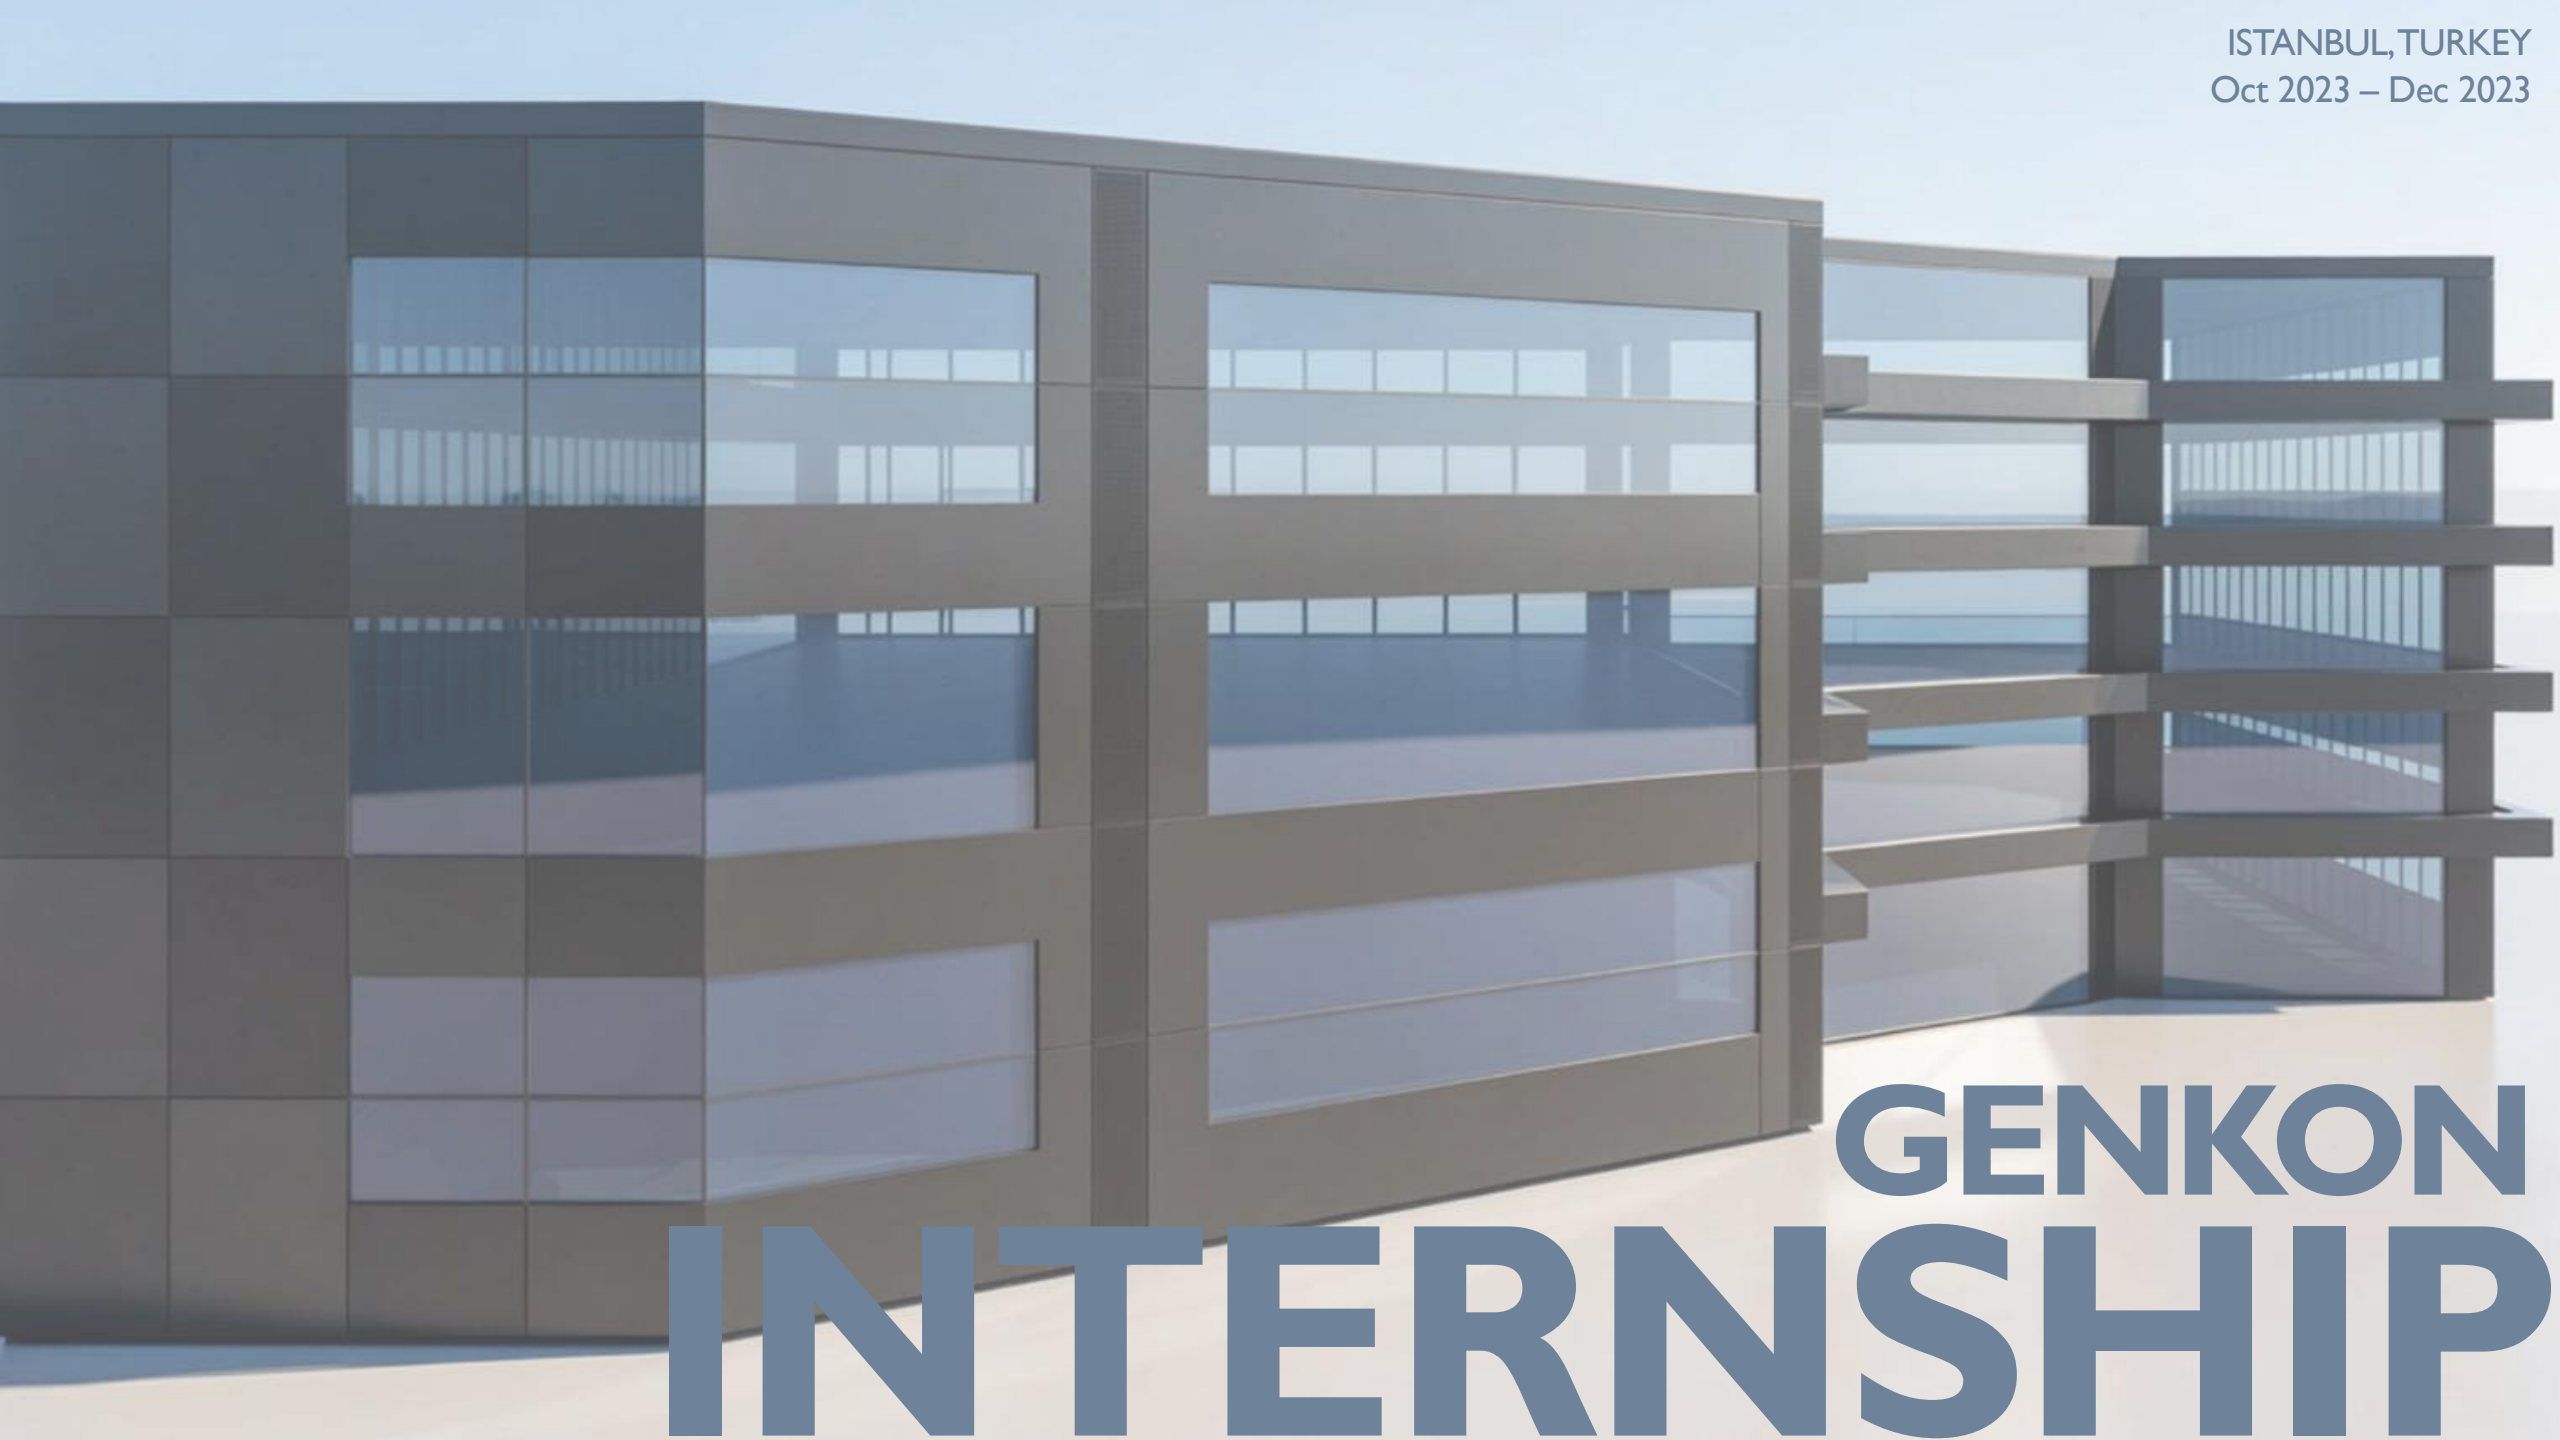

GENKON
INTERNSHIP

SITE PLAN + INITIAL IDEAS

Initial Floor Plans - Sketch on AutoCAD

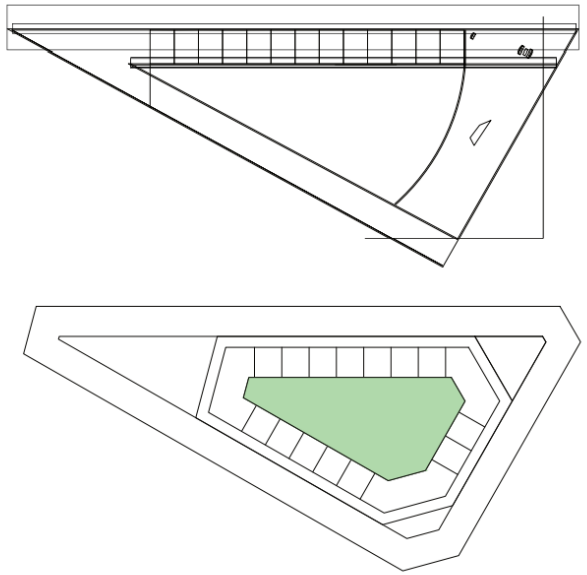


Istanbul, Turkey
INTERNSHIP

Derin ENHOŞ
Stajyer Mimar / Trainee Architect
GENKON
Küçükbakkalköy Mah. Selvili Sok. Canan Business No:4 Kat:1
Ataşehir / İstanbul / TÜRKİYE
Web : www.genkon.com.tr
Tel :+90 216 3800140 (pbx)
E-posta : derinos@genkon.com.tr

Site Plan

Scale: 1:1000

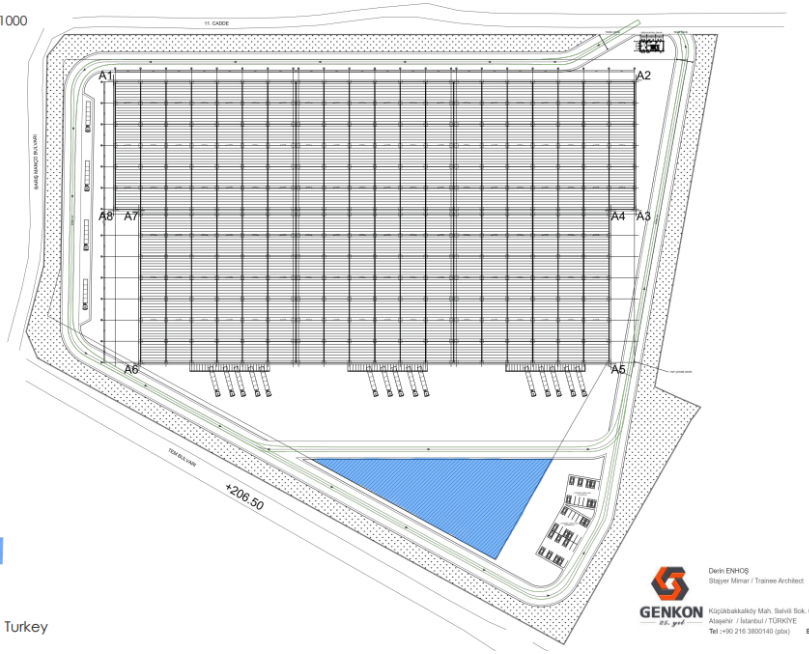


Istanbul, Turkey
INTERNSHIP

Derin ENHOŞ
Stajyer Mimar / Trainee Architect
GENKON
Küçükbakkalköy Mah. Selvili Sok. Canan Business No:4 Kat:1
Ataşehir / İstanbul / TÜRKİYE
Web : www.genkon.com.tr
Tel :+90 216 3800140 (pbx)
E-posta : derinos@genkon.com.tr

INITIAL DESIGN IDEAS

Initial Design - Floor Plans


Scale: 1:200
Floors 1-5

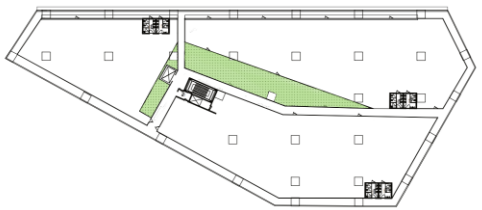

Istanbul, Turkey

Improving the Initial Design

Scale: 1:200
Ground Floor Plan

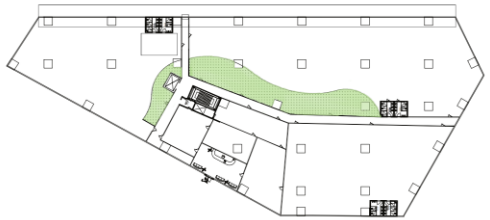

Istanbul, Turkey

Initial Design - Floor Plans


Scale: 1:200
Underground car park, 126 parking spaces.



Istanbul, Turkey

Initial Design - Floor Plans

Scale: 1:200
Ground Floor Plan

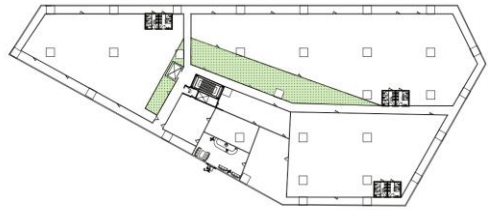


Istanbul, Turkey

THE DESIGN PROCESS

The Design Process


Scale: 1:200
Ground Floor Plan testing different forms and how it works with columns

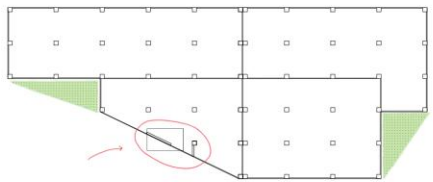

Istanbul, Turkey

The Design Process


Scale: 1:200
Ground Floor Plan testing different forms and how it works with columns

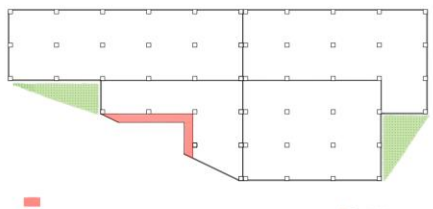

Istanbul, Turkey

The Design Process

Scale: 1:200
Ground Floor Plan testing different forms and how it works with columns

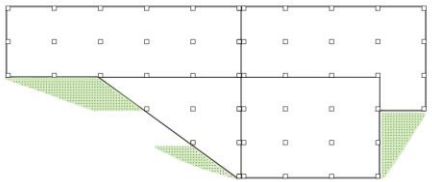

Istanbul, Turkey

Correcting the Form

Scale: 1:200
Columns - resized and finalised




Istanbul, Turkey

FINAL IDEAS

Final Design - Floor Plans


Scale: 1:200
Floors 1-5

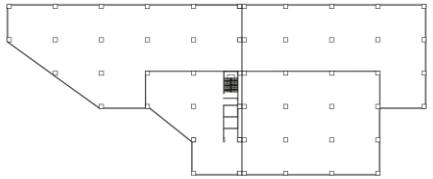

Istanbul, Turkey

Example Interior for Final Floor Plan


Scale: 1:200

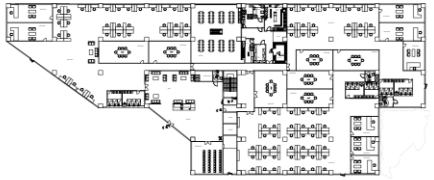

Istanbul, Turkey

Final Design - Floor Plans


Scale: 1:200
Underground car park, 100 parking spaces.

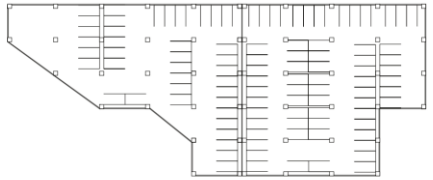

Istanbul, Turkey

Final Design - Floor Plans

Scale: 1:200
Ground Floor Plan

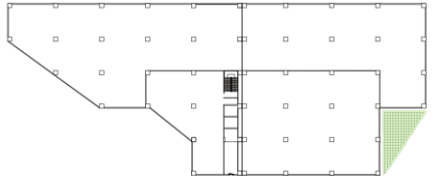


Istanbul, Turkey


OFFICE DESIGN FOR PARTAŞ

During my 2-month internship at **GENKON Engineering Istanbul**, our team of architects and engineers collaborated on a project to design an office space adjacent to the administrative building in Bahçelievler, situated in Kapaklı, Tekirdağ, on the European continent of Istanbul for a construction company called Partaş.


Example floor plan of the building including interior designed by myself:

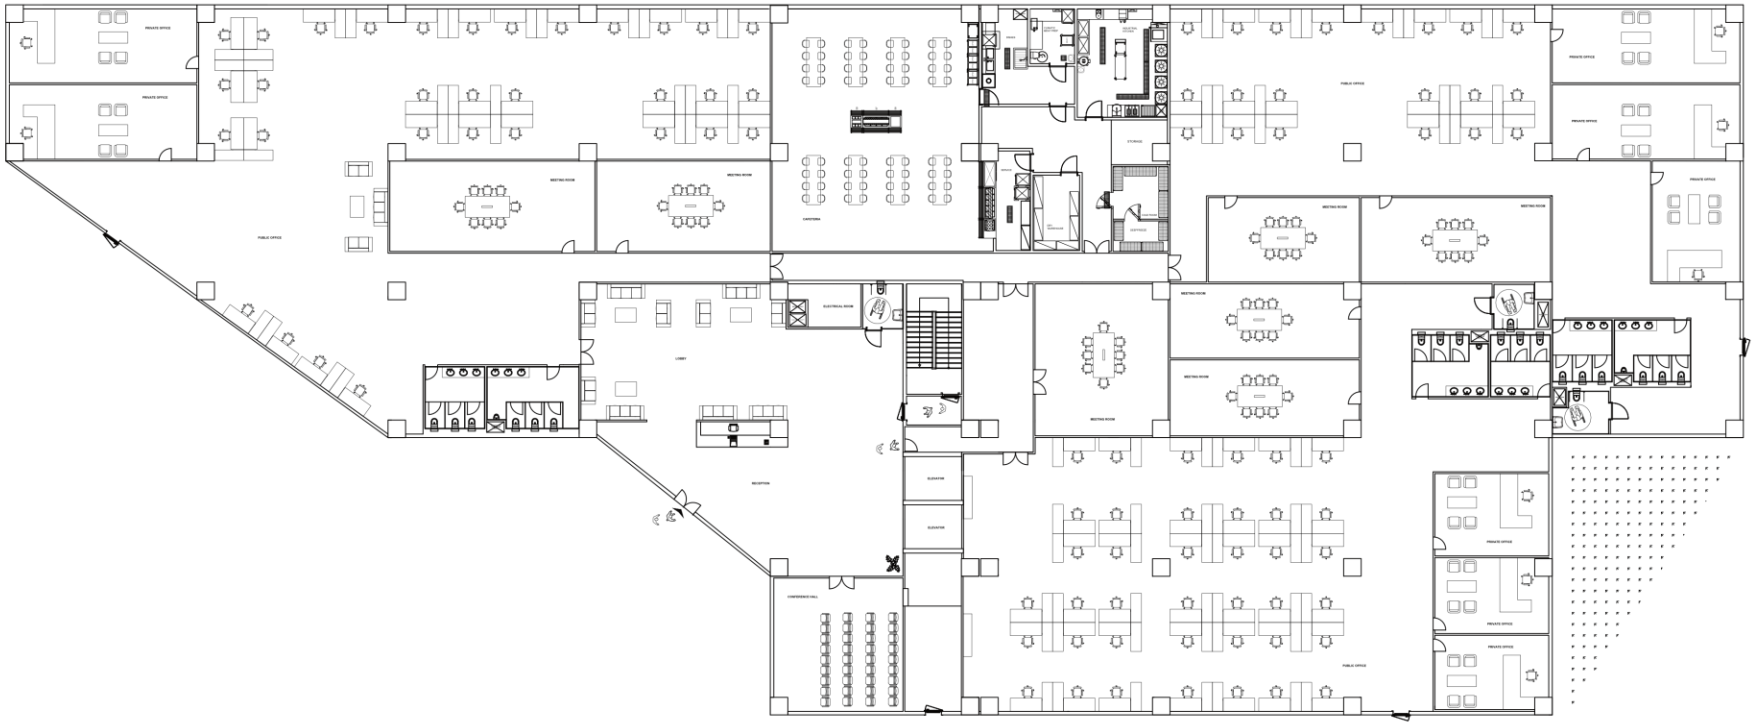

Examples of floor plans from the design process:

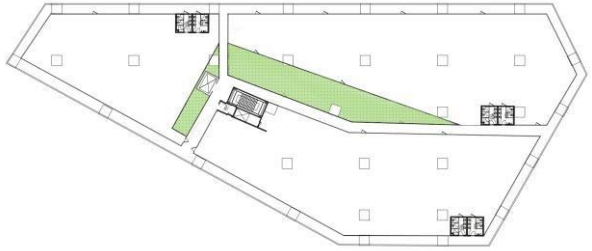



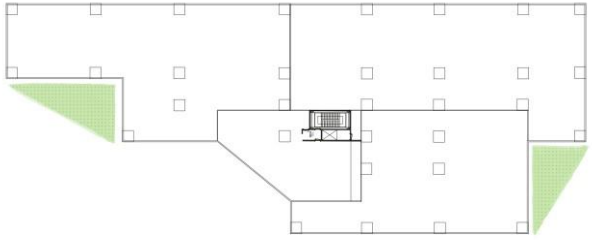


Throughout this experience, I acquired invaluable skills, including proficiency in AutoCAD and the integration of structural elements such as columns into floor plans. Moreover, I gained insights into the critical aspect of communicating designs effectively in a language comprehensible to engineers.

Our focus extended beyond mere aesthetics; we prioritized the practicality of the building's layout while adhering to engineering constraints and ensuring feasibility within real-world parameters. This emphasis on pragmatic design solutions underscored the importance of balancing creativity with functionality, a lesson I continue to carry with me in my architectural endeavors.

Derin ENHOŞ
Stajyer Mimar / Trainee Architect
GENKON
Küçükbakkalköy Mah. Selvili Sok. Canan Business No:4 Kat:1
Ataşehir / İstanbul / TÜRKİYE
Web : www.genkon.com.tr
Tel :+90 216 3800140 (pbx)
E-posta : denhos@genkon.com.tr


Showing how the example design fits the site.

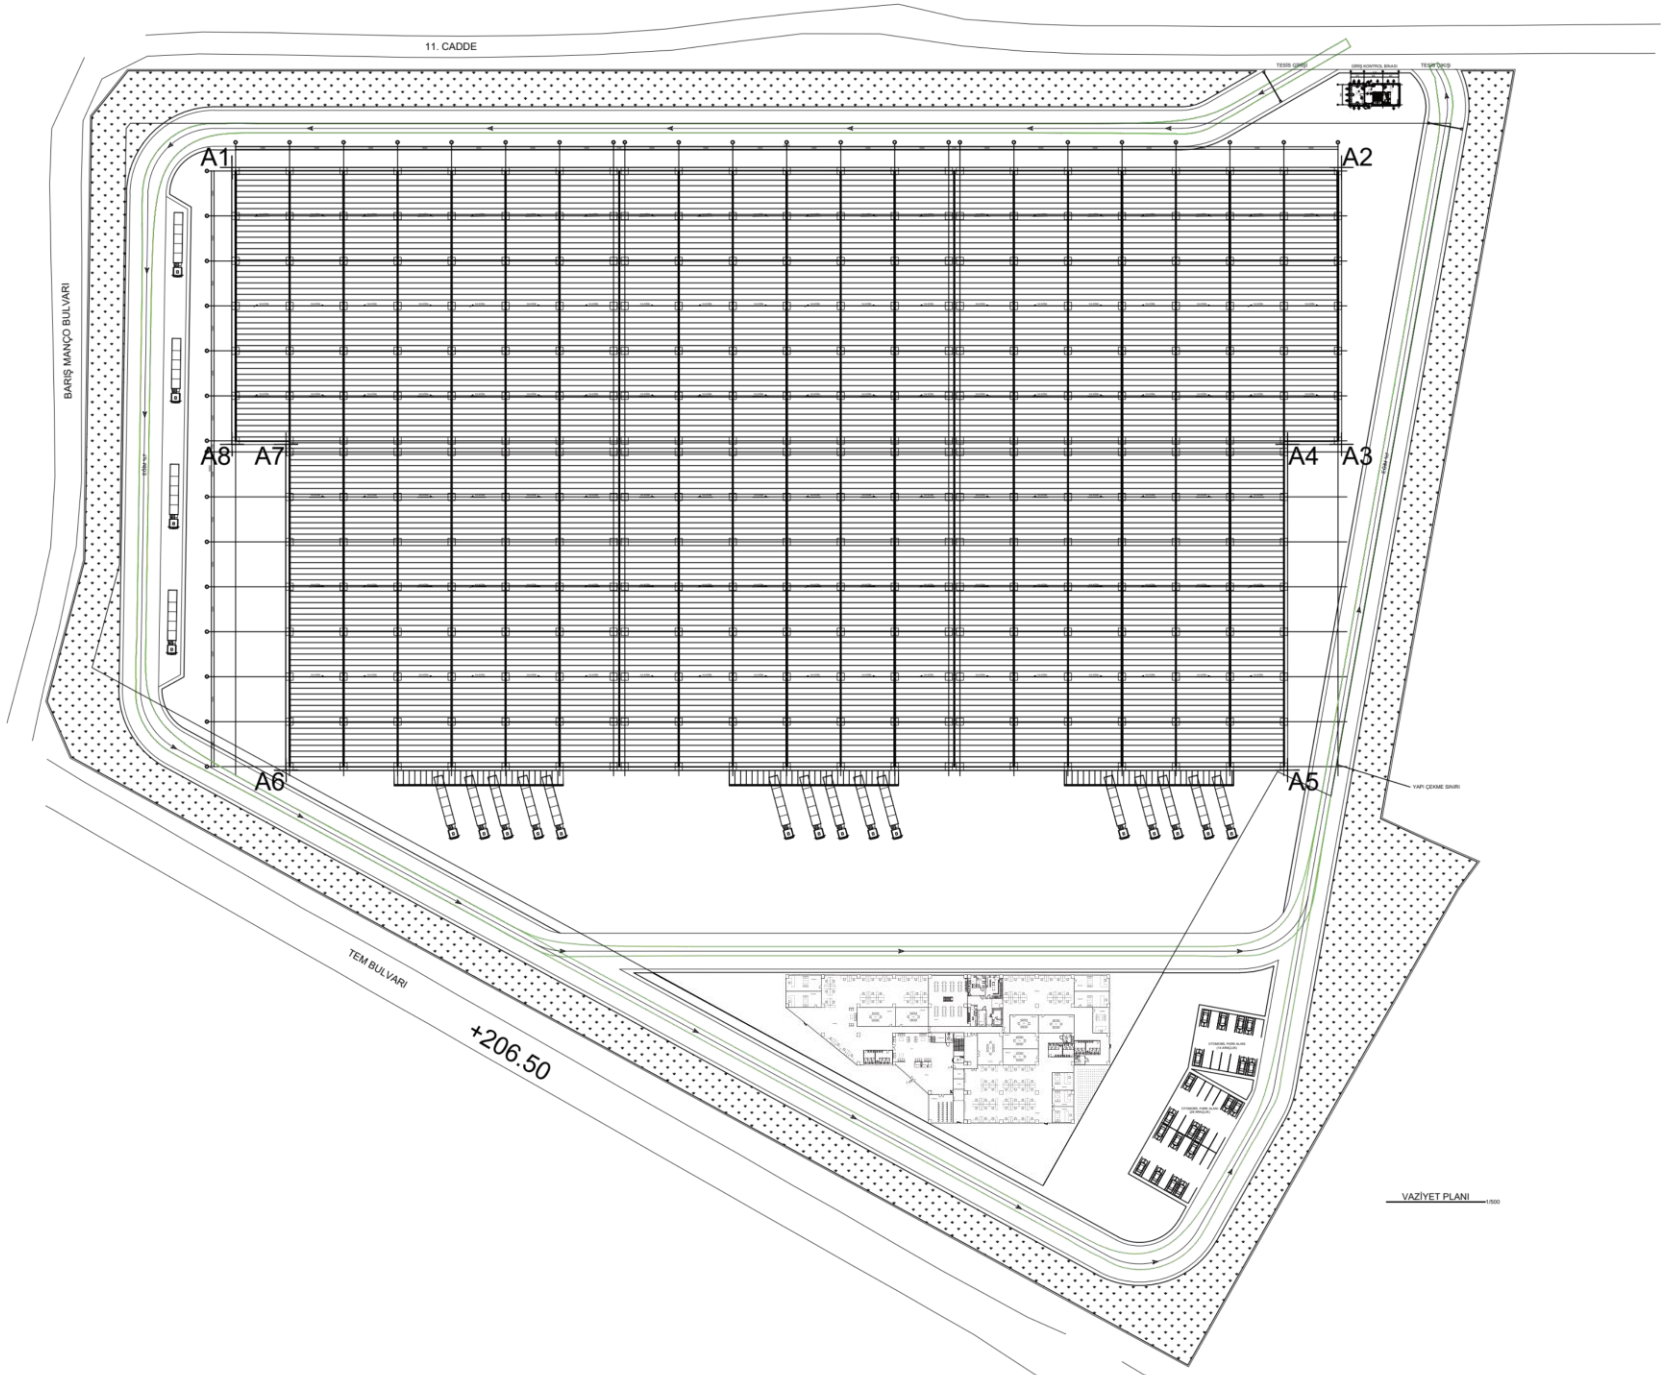



Derin ENHOŞ
Stajyer Mimar / Trainee Architect
GENKON
Küçükbakkalköy Mah. Selvili Sok. Canan Business No:4 Kat:1
Ataşehir / İstanbul / TÜRKİYE
Web : www.genkon.com.tr
Tel :+90 216 3800140 (pbx)
E-posta : denhos@genkon.com.tr

OFFICE DESIGN – SKETCHUP MODEL


In addition to brainstorming and creating floor plans on **AutoCAD**, I took charge of modeling the final design using **SketchUp**, a crucial step in providing clients with realistic visualizations. I meticulously crafted detailed **3D models**, collaborating closely with the rendering team to produce photorealistic renderings that enhanced the visual appeal of our designs. This multifaceted role highlighted my adaptability and proficiency in utilizing various tools to bring our creative vision to life, resulting in designs that exceeded client expectations. I have included my **SketchUp** model as an example here.

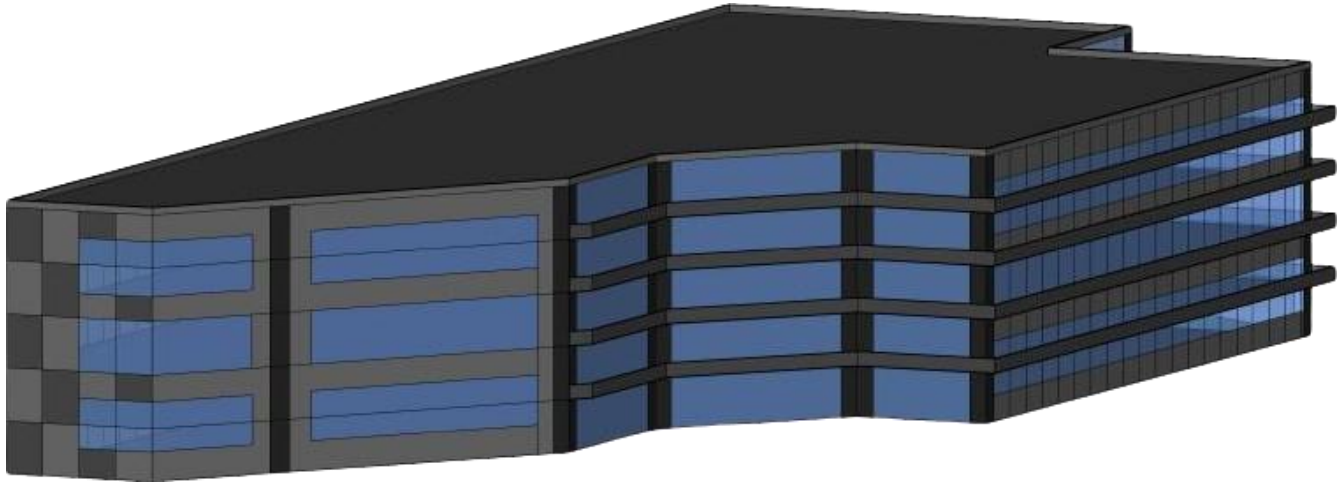


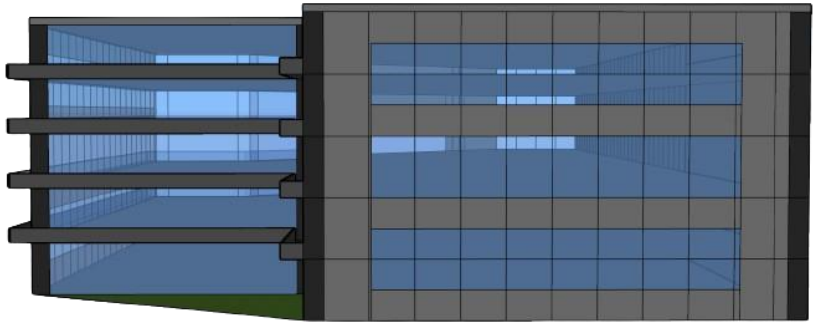


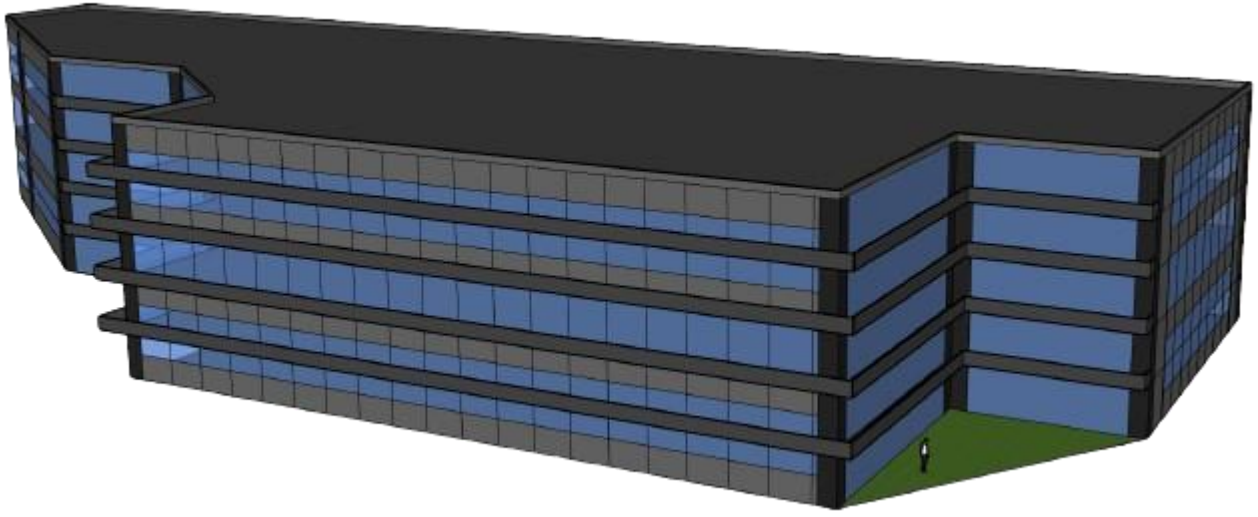


Derin ENHOŞ
Stajyer Mimar / Trainee Architect
GENKON
Küçükbakkalköy Mah. Selvili Sok. Canan Business No:4 Kat:1
Ataşehir / İstanbul / TÜRKİYE
Web : www.genkon.com.tr
Tel :+90 216 3800140 (pbx)
E-posta : denhos@genkon.com.tr

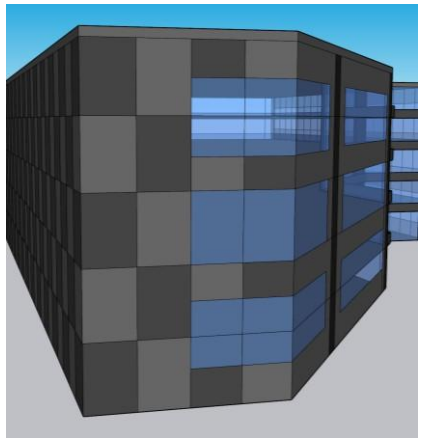

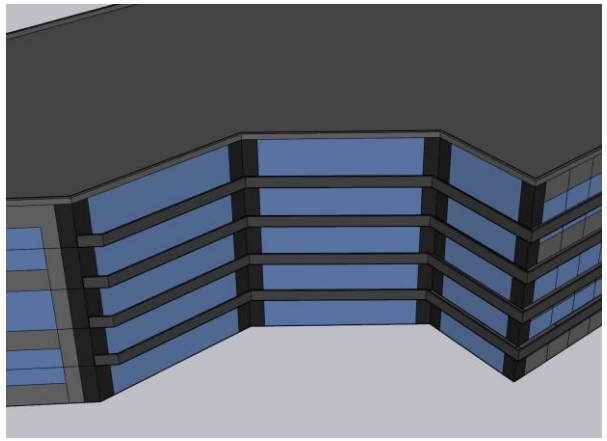


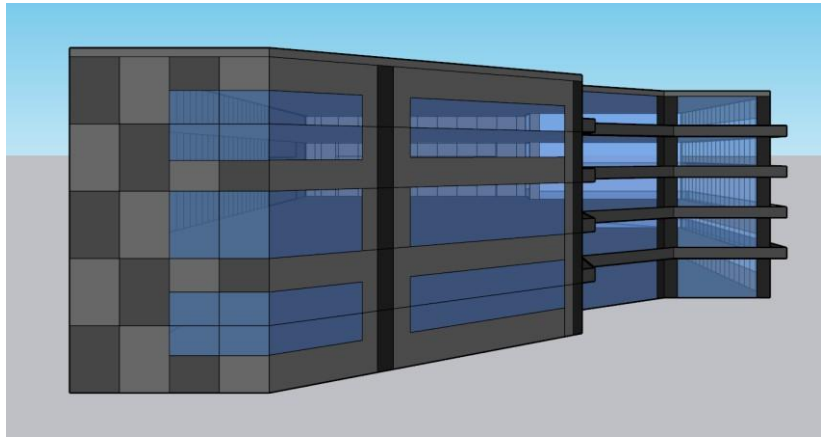


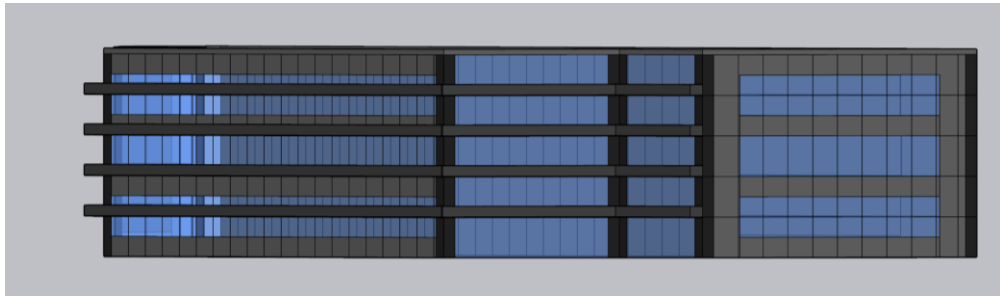



Derin ENHOŞ
Stajyer Mimar / Trainee Architect

GENKON
25. yıl
Küçükbakkalköy Mah. Selvili Sok. Canan Business No:4 Kat:1
Ataşehir / İstanbul / TÜRKİYE
Tel : +90 216 3800140 (pbx)
Web : www.genkon.com.tr
E-posta : denhos@genkon.com.tr

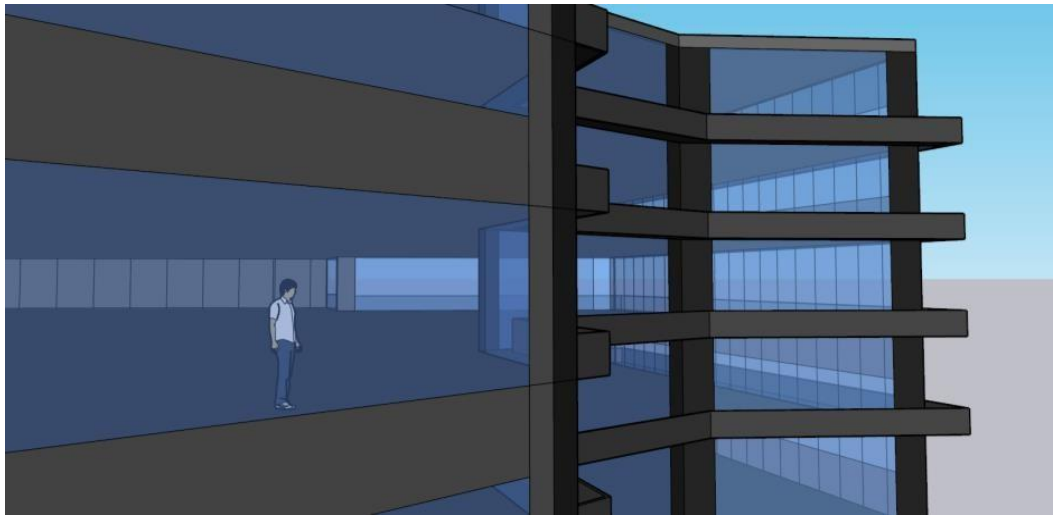

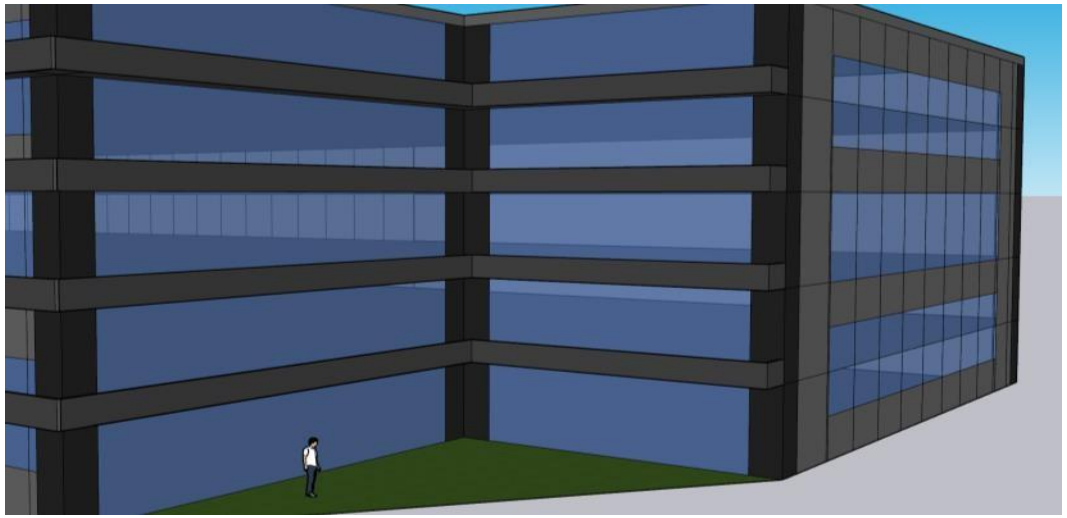

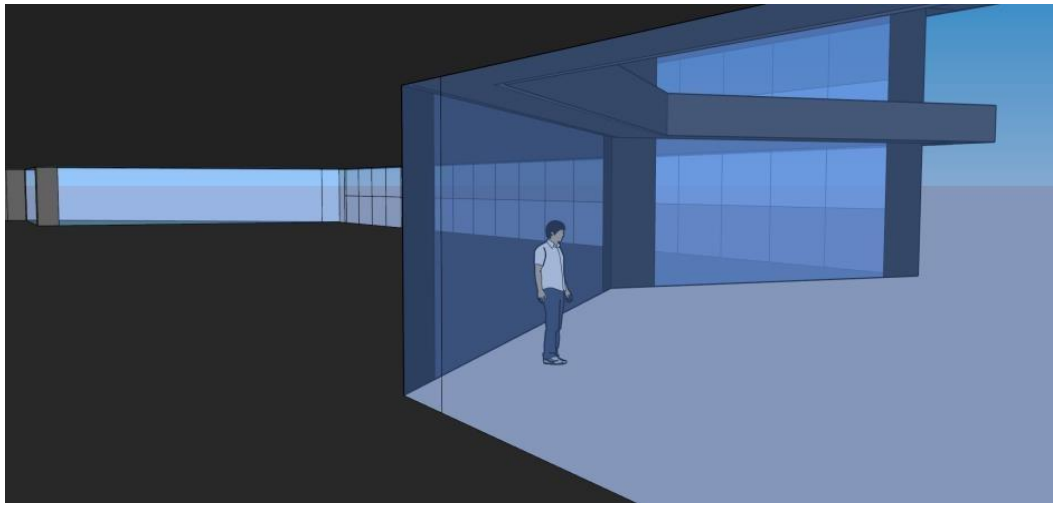

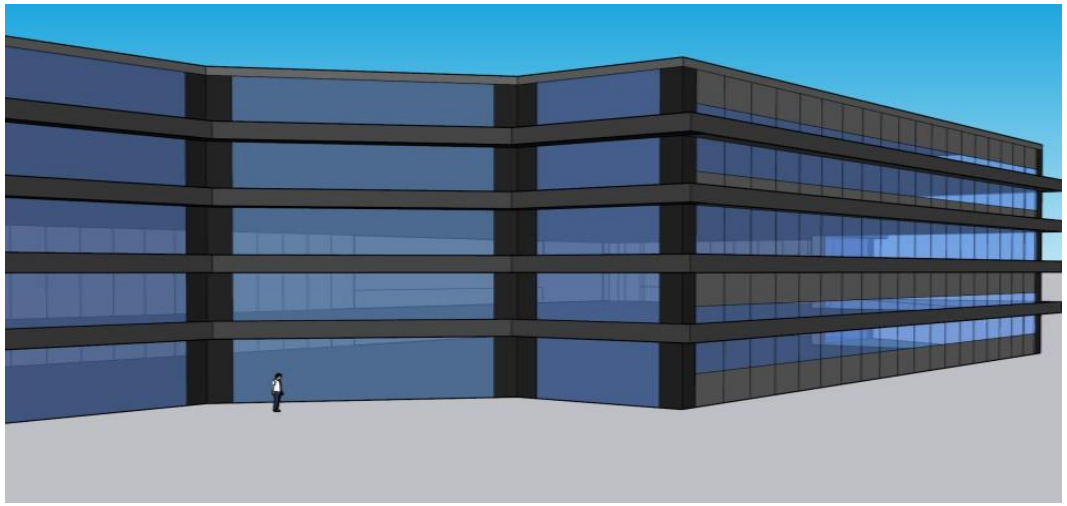

Derin ENHOŞ
Stajyer Mimar / Trainee Architect


GENKON
25. yıl

Küçükbakkalköy Mah. Selvili Sok. Canan Business No:4 Kat:1
Ataşehir / İstanbul / TÜRKİYE
Web : www.genkon.com.tr
Tel :+90 216 3800140 (pbx)
E-posta : denhos@genkon.com.tr


LONDON, UK
July 2021 – Aug 2021

INVESTIN
INTERNSHIP

INVESTIN YOUNG ARCHITECTS SUMMER INTERNSHIP

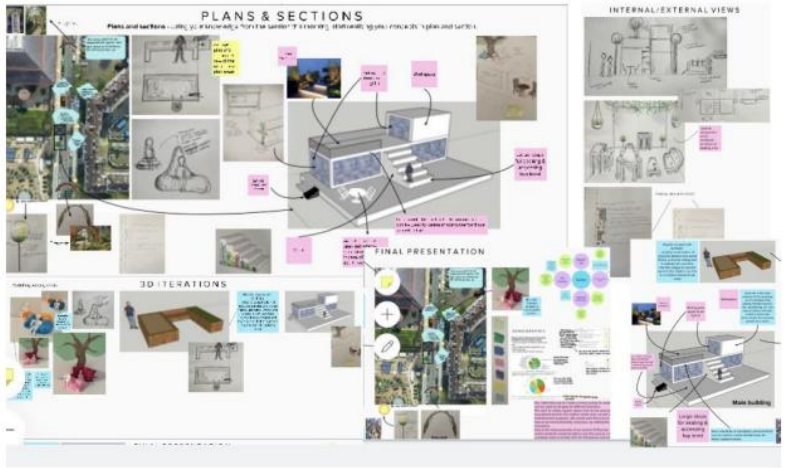



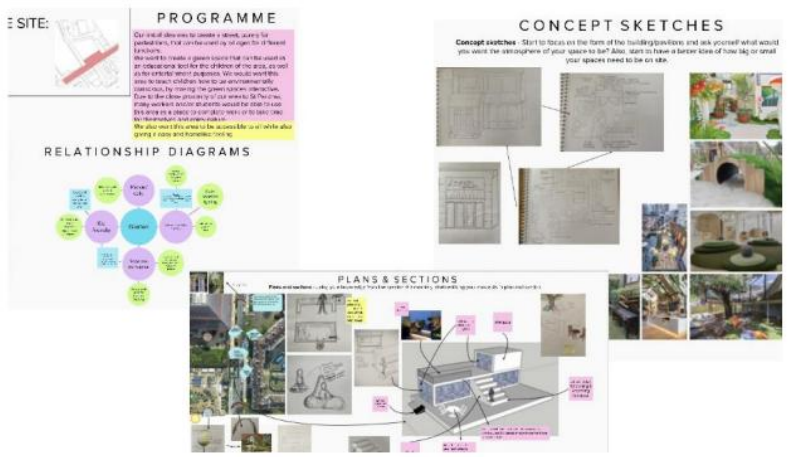


INVESTIN
Certificate of Completion
THIS CERTIFICATE IS PROUDLY PRESENTED TO
Derin Enhos
August 6, 2021
FOR COMPLETING
THE YOUNG ARCHITECT SUMMER INTERNSHIP
2021

DUBAI, UAE
Aug 2020

architecture
interiors L.L.C

INTERNSHIP

Client + Context

About my Client

Name: Cem Kapancıoğlu
Company: CK Architecture & Interiors
Position within the company: Managing Director

Personal Design Style?

"I wouldn't really say I have a personal Interior Design style. I would follow contemporary modern design methodology. I find minimalist contemporary modern design less appealing."

Project Context:

The company is relocating in Dubai, UAE, from the Deyaar Building next to the Mall of Emirates to The Greens area. The office is getting upgraded furniture and an updated design that is a pleasant place to work in and have client meetings.

***My Client's Request**: To design an office table to be used as his main workspace and for meetings.*

Preferences for features of the table:

Dark hardwood – maybe mahogany, maple or oak.

T-shaped table that will be joint with a meeting table for client meetings.

Needs something unique that would complement the room that has a marble accent wall as well as giving a good image to the clients, showing off his personality.

Deals with billionaire clients – Must make a good impression.



Company Research

Here's a link to their website: https://www.ckarchitecture.com

Some of their projects that I personally find very impressive:



Tetrapak Innovation Centre-CIC Dubai

Commercial:

- Tetrapak Innovation Centre-CIC Dubai - has a colorful and creative design which matches very well with the company's goal of promoting innovation.



VIP Turkish Hammam & Villa

Residential:

- VIP Turkish Hammam & Villa – takes inspiration from the Ottoman Empire's ancient architecture that complements the concept of the Hammam treatments in a Turkish bath associated with the Islamic world.

Company size: 51-200 employees.

Founded in year 2010

"I founded CK Architecture Interiors in Dubai in 2010. My vision was to create a vertically integrated design and build boutique specialist in the creation of opulent living and working spaces. I wanted it to be different." – Mr. Cem Kapancıoğlu.

"the world would be a better place if only we could respect and protect nature by considering ourselves as an integral part of it, not the owners of it." – Mr. Cem Kapancıoğlu.

IDEA 1











IDEA 2











IDEA 3












Materials

- Marble
- Stained Maple Wood
- Plexiglass/Clear Acrylic
- Metal
- Epoxy Resin

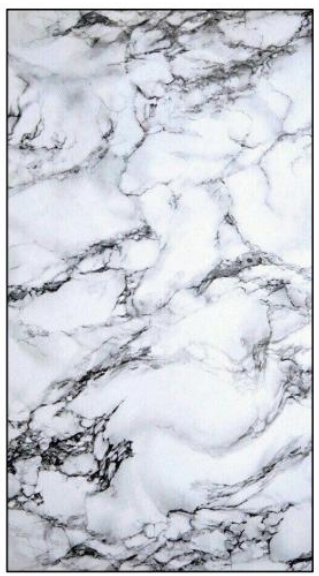



Why Maple wood?

- Hardwood – Perfect for furniture
- Affordable – Average price of $7 - $11 per square foot for materials and installation.
- Durable – Hard to dent, etc.
- Can be stained:

(Colour range: cream to reddish brown)

Epoxy Resin Pros:

- Durable resin finish - When epoxy hardens, it creates a solid surface that should last for years.
- High-Gloss finish. Leaves a super-shiny and glossy polished finish.
- Unlimited design potential.
- Heat resistant.
- Nontoxic and food safe.
- Easy to clean.